


AVONLEA PHASE 1

(A HAMLET SUBDIVISION)
SECTION 35, TOWNSHIP 16 SOUTH, RANGE 23 EAST &
SECTION 2, TOWNSHIP 17 SOUTH, RANGE 23 EAST,
MARION COUNTY, FLORIDA

PLAT BOOK 10, PAGE 195

SHEET 1 OF 9

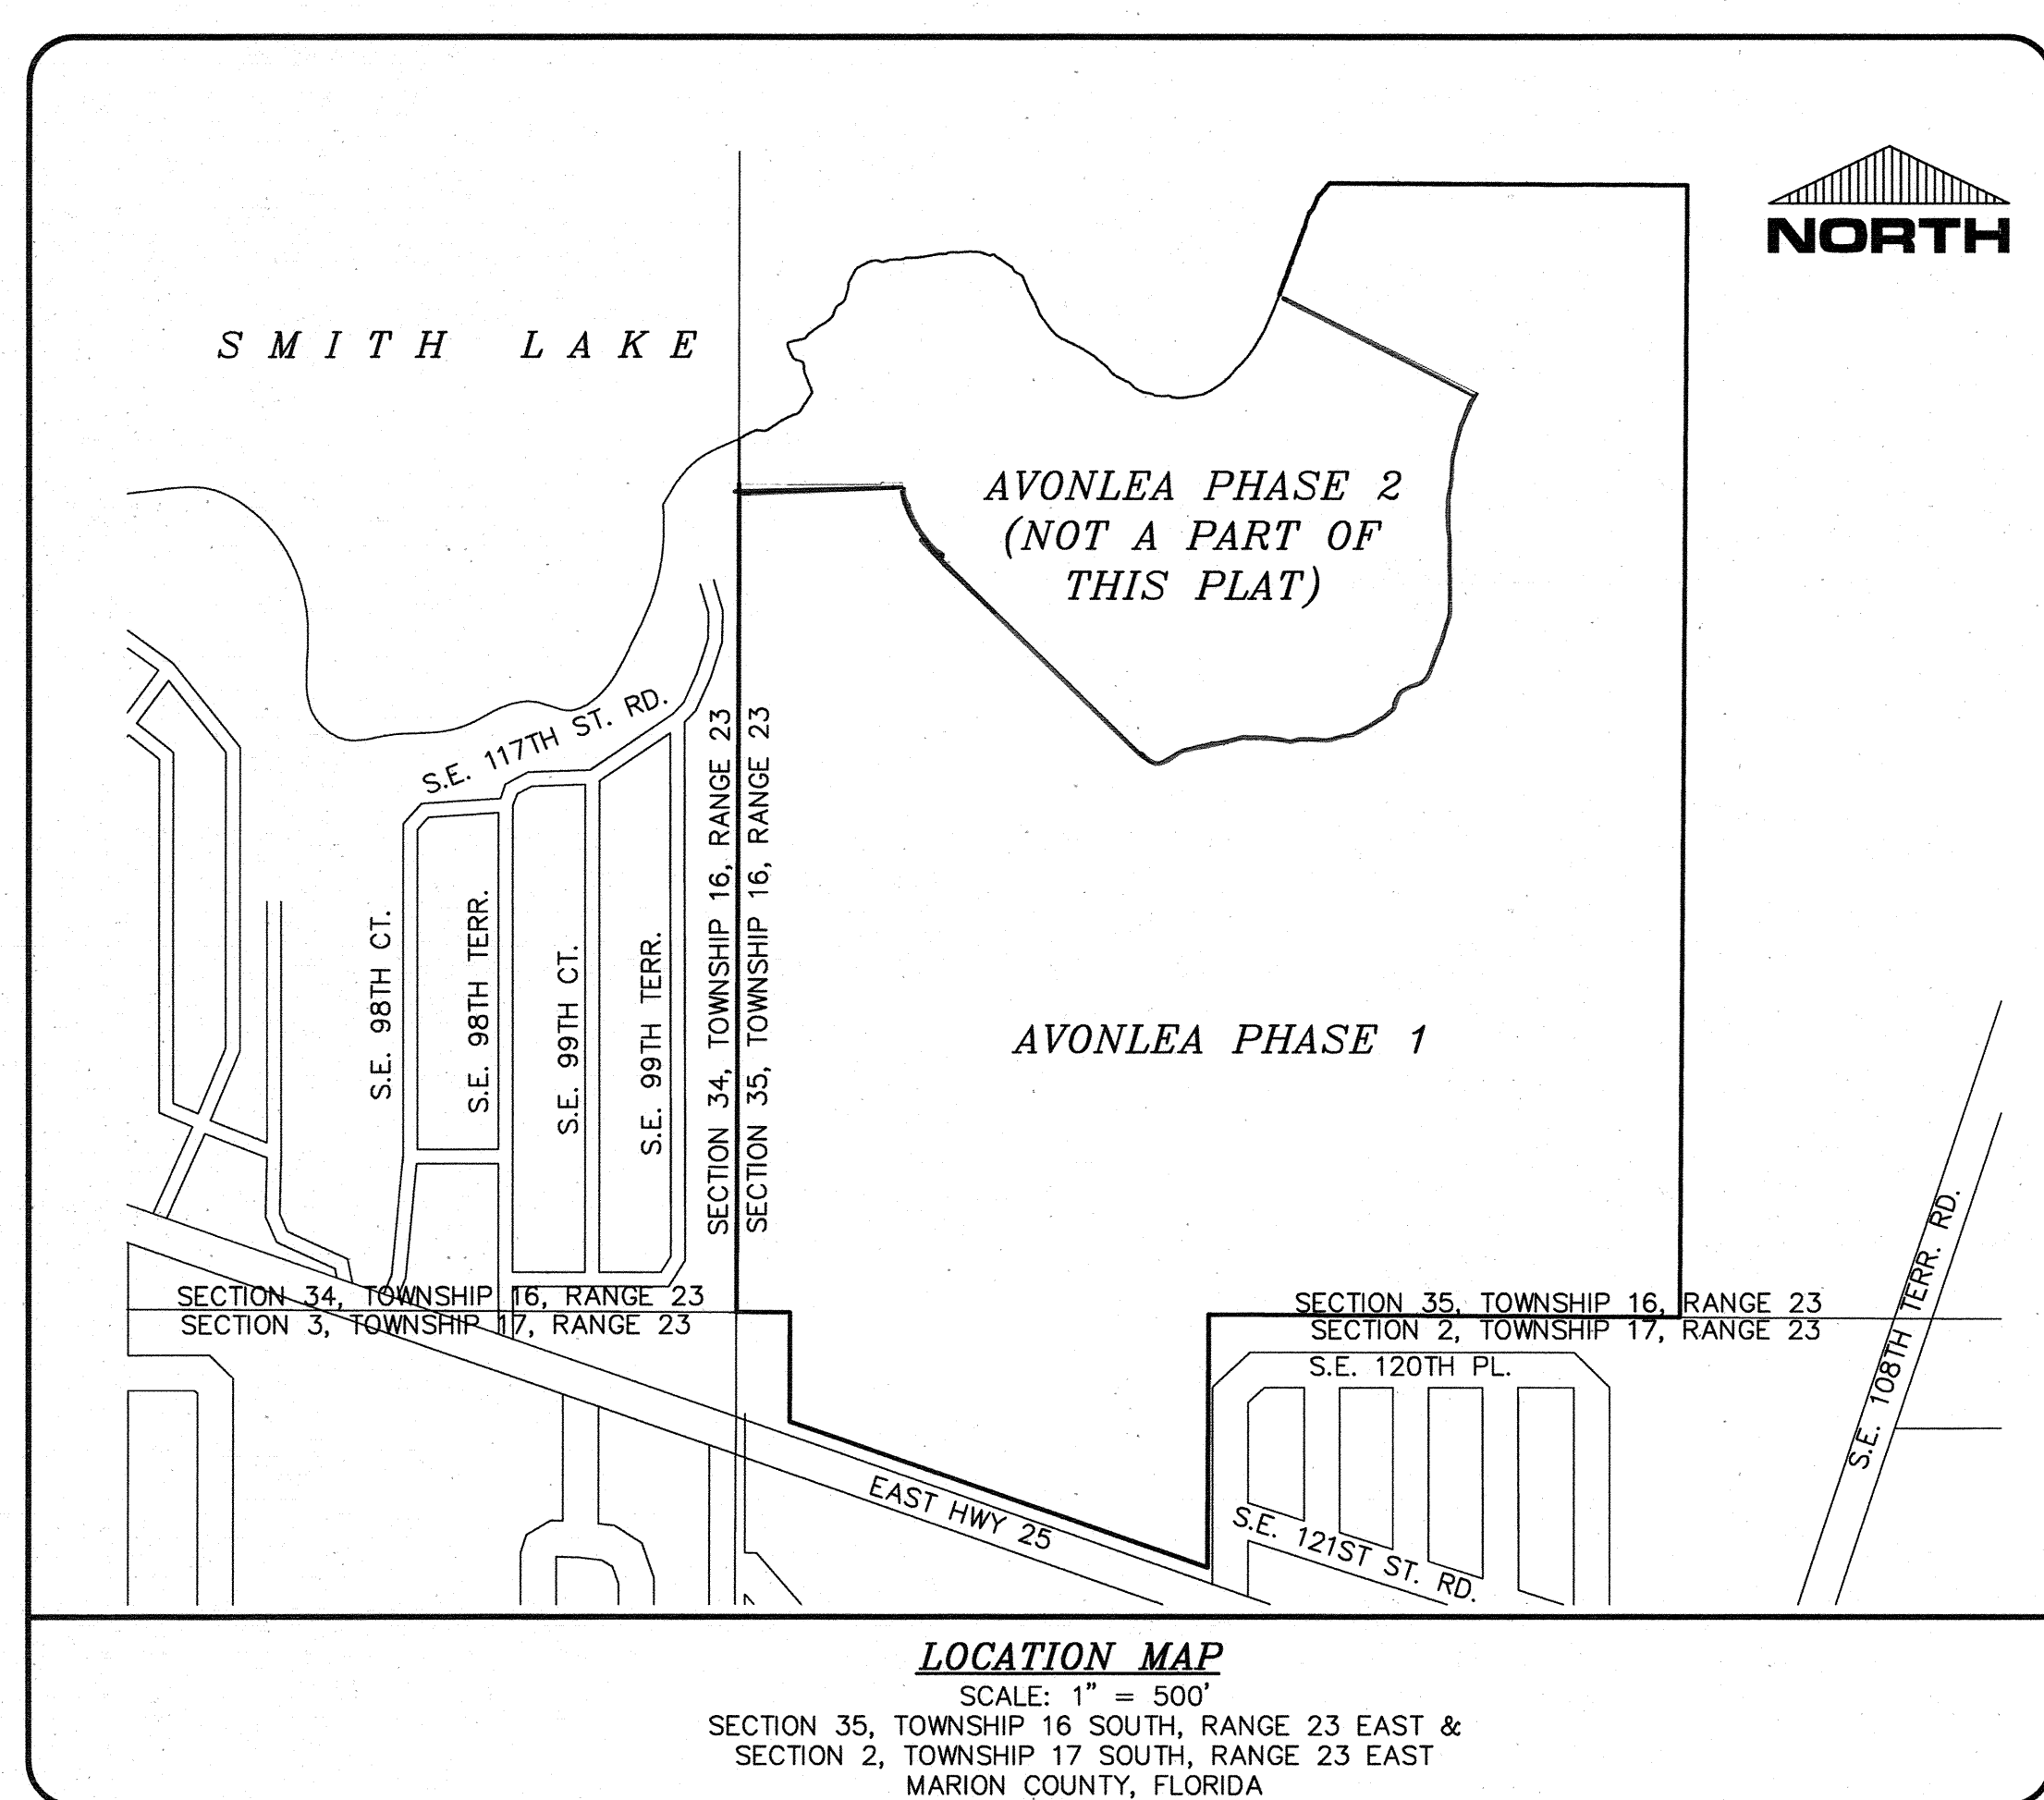

DESCRIPTION:

A PORTION OF GOVERNMENT LOT 3, AND ALSO GOVERNMENT LOT 4 ALL BEING IN SECTION 35, TOWNSHIP 16 SOUTH, RANGE 23 EAST; AND ALSO THE N.W. 1/4 OF THE N.W. 1/4 LYING NORTH OF DIXIE HIGHWAY IN SECTION 2, TOWNSHIP 17 SOUTH, RANGE 23 EAST MORE PARTICULARLY DESCRIBED AS FOLLOWS:

BEGIN AT THE SOUTHEAST CORNER OF THE S.E. 1/4 OF THE S.W. 1/4 OF SECTION 35, TOWNSHIP 16 SOUTH, RANGE 23 EAST, THENCE N.89°41'35"W., ALONG THE SOUTH BOUNDARY OF THE S.E. 1/4 OF THE S.W. 1/4 OF SAID SECTION 35, A DISTANCE OF 1323.49 FEET TO THE SOUTHWEST CORNER OF THE S.E. 1/4 OF THE S.W. 1/4 OF SAID SECTION 35; THENCE S.00°11'13"W., ALONG THE EAST BOUNDARY OF THE N.W. 1/4 OF THE N.W. 1/4 OF SECTION 2, TOWNSHIP 17 SOUTH, RANGE 23 EAST, A DISTANCE OF 709.62 FEET TO THE NORTH RIGHT OF WAY LINE OF EAST HIGHWAY 25; THENCE N.70°50'06"W., ALONG THE NORTH RIGHT OF WAY OF SAID EAST HIGHWAY 25, A DISTANCE OF 1243.08 FEET; THENCE DEPARTING SAID RIGHT OF WAY N.00°08'44"E., A DISTANCE OF 307.83 FEET TO THE NORTH BOUNDARY OF N.W. 1/4 OF SECTION 2, TOWNSHIP 17 SOUTH, RANGE 23 EAST; THENCE N.89°41'35"W., ALONG THE NORTH BOUNDARY OF SAID SECTION 2, A DISTANCE OF 150.01 FEET TO THE NORTHWEST CORNER OF N.W. 1/4 OF SAID SECTION 2, ALSO BEING THE S.W. CORNER OF GOVERNMENT LOT 4; THENCE N.00°08'23"E., ALONG THE WEST BOUNDARY OF SAID GOVERNMENT LOT 4, A DISTANCE OF 2324.63 FEET; THENCE DEPARTING SAID WEST BOUNDARY S.89°51'55"E., A DISTANCE OF 399.85 FEET TO THE POINT OF CURVATURE OF A NON-TANGENT CURVE CONCAVE EASTERLY, HAVING A CENTRAL ANGLE OF 01°00'31", A RADIUS OF 305.00 FEET AND A CHORD OF 5.37 FEET, BEARING N.00°22'10"W.; THENCE NORTHERLY ALONG THE ARC OF SAID CURVE, A DISTANCE OF 5.37 FEET TO THE END OF SAID CURVE; THENCE S.89°51'55"E., A DISTANCE OF 60.00 FEET TO THE POINT OF CURVATURE OF A CURVE CONCAVE NORTHEASTERLY, HAVING A CENTRAL ANGLE OF 45°48'09", A RADIUS OF 245.00 FEET, AND A CHORD OF 190.68 FEET BEARING S.22°46'00"E.; THENCE SOUTHEASTERLY ALONG THE ARC OF SAID CURVE, A DISTANCE OF 195.85 FEET TO THE POINT OF TANGENCY; THENCE S.45°40'04"E., A DISTANCE OF 864.94 FEET TO THE POINT OF CURVATURE OF A CURVE CONCAVE NORTHERLY, HAVING A CENTRAL ANGLE OF 77°05'32", A RADIUS OF 25.00 FEET, AND A CHORD OF 31.16 FEET BEARING N.84°12'50"E.; THENCE EASTERLY ALONG THE ARC OF SAID CURVE, A DISTANCE OF 33.64 FEET TO THE POINT OF REVERSE CURVATURE OF A CURVE CONCAVE SOUTHERLY, HAVING A CENTRAL ANGLE OF 33°38'30", A RADIUS OF 400.00 FEET, AND A CHORD OF 231.50 FEET, BEARING N.74°03'39"E.; THENCE EASTERLY ALONG THE ARC OF SAID CURVE, A DISTANCE OF 234.86 FEET TO THE POINT OF TANGENCY; THENCE S.89°07'06"E., A DISTANCE OF 183.64 FEET TO THE POINT OF CURVATURE OF A CURVE CONCAVE NORTHERLY, HAVING A CENTRAL ANGLE OF 36°00'42", A RADIUS OF 400.00 FEET, AND A CHORD OF 247.29 FEET BEARING N.72°52'33"E.; THENCE EASTERLY ALONG THE ARC OF SAID CURVE, A DISTANCE OF 251.41 FEET TO THE POINT OF COMPOUND CURVATURE OF A CURVE CONCAVE NORTHWESTERLY, HAVING A CENTRAL ANGLE OF 54°28'00", A RADIUS OF 25.00 FEET, AND A CHORD OF 22.88 FEET BEARING N.27°38'12"E.; THENCE NORTHEASTERLY ALONG THE ARC OF SAID CURVE, A DISTANCE OF 23.77 FEET TO THE POINT OF REVERSE CURVATURE OF A CURVE CONCAVE SOUTHEASTERLY, HAVING A CENTRAL ANGLE OF 90°25'10", A RADIUS OF 60.00 FEET, AND A CHORD OF 85.16 FEET BEARING N.45°36'47"E.; THENCE NORTHEASTERLY ALONG THE ARC OF SAID CURVE, A DISTANCE OF 94.69 FEET TO THE POINT OF REVERSE CURVATURE OF A CURVE CONCAVE NORTHWESTERLY, HAVING A CENTRAL ANGLE OF 54°28'00", A RADIUS OF 25.00 FEET, AND A CHORD OF 22.88 FEET BEARING N.63°35'22"E.; THENCE NORTHEASTERLY ALONG THE ARC OF SAID CURVE, A DISTANCE OF 23.77 FEET TO THE POINT OF COMPOUND CURVATURE OF A CURVE CONCAVE NORTHWESTERLY, HAVING A CENTRAL ANGLE OF 36°00'42", A RADIUS OF 400.00 FEET, AND A CHORD OF 247.29 FEET BEARING N.18°21'01"E.; THENCE NORTHERLY ALONG THE ARC OF SAID CURVE, A DISTANCE OF 251.41 FEET TO THE POINT OF TANGENCY; THENCE N.00°20'40"E., A DISTANCE OF 288.14 FEET TO THE POINT OF CURVATURE OF A CURVE CONCAVE SOUTHEASTERLY, HAVING A CENTRAL ANGLE OF 26°13'14", A RADIUS OF 560.00 FEET, AND A CHORD OF 254.05 FEET BEARING N.13°27'17"E.; THENCE NORTHERLY ALONG THE ARC OF SAID CURVE, A DISTANCE OF 256.28 FEET TO THE POINT OF TANGENCY; THENCE N.26°33'54"E., A DISTANCE OF 41.68 FEET; THENCE N.63°26'06"W., A DISTANCE OF 623.30 FEET TO THE ORDINARY HIGH WATER LINE OF SMITH LAKE AS ESTABLISHED BY THE DEPARTMENT OF ENVIRONMENTAL PROTECTION, BASED ON ELEVATION 52.76 FEET (N.A.V.D. 88); THENCE NORTHEASTERLY ALONG AND WITH SAID ORDINARY HIGH WATER LINE, THROUGH A BEARING OF N.24°01'29"E., A DISTANCE OF 346.02 FEET; THENCE DEPARTING SAID ORDINARY HIGH WATER LINE, S.89°39'20"E., A DISTANCE OF 1004.15 FEET TO THE EAST BOUNDARY OF GOVERNMENT LOT 3; THENCE S.00°20'40"W., ALONG THE EAST BOUNDARY OF SAID GOVERNMENT LOT 3, A DISTANCE OF 3179.30 FEET TO THE POINT OF BEGINNING. SAID LANDS BEING SITUATED IN MARION COUNTY, FLORIDA, CONTAINING 152.60 ACRES MORE OR LESS.

LOCATION MAP

SCALE: 1" = 500'
SECTION 35, TOWNSHIP 16 SOUTH, RANGE 23 EAST &
SECTION 2, TOWNSHIP 17 SOUTH, RANGE 23 EAST
MARION COUNTY, FLORIDA

R.M. BARRINEAU & ASSOCIATES, INC.

PROFESSIONAL SURVEYORS & MAPPERS
OAKHURST PROFESSIONAL PARK
1309 S.E. 25TH LOOP, SUITE 103 PHONE (352) 622-3133
OCALA, FLORIDA 34471 FAX (352) 369-3771
REGINALD M. BARRINEAU, P.S.M. - FOUNDER
CERTIFICATE OF AUTHORIZATION NO. LB 5091
KEVIN J. FLANAGAN, P.S.M. - LS 3942 CHRISTOPHER J. HOWSON, P.S.M. - LS 6553
MELVIN A. BOWEN, P.S.M. - LS 5035

APPROVED WAIVERS:

NO.	ITEM	SECTION & 1/4 SECTION LINE DEDICATIONS	APPROVAL DATE
1)	8.2.5.a(2)(d)ii	CUL DE SAC LENGTH	08-01-05
2)	8.2.5.a(3)	BLOCK LENGTH	08-01-05
3)	8.2.5.a(4)	RETENTION BASIN SIGNAGE	08-01-05
4)	8.2.9.d(6)(1)	ACCESS TO ADJACENT LANDS	08-01-05
5)	8.2.5.a(14)	BUFFERING	08-01-05
6)	8.2.10.k(4)(c)iii	POTABLE WATER SERVICE CRITERIA	09-20-05 (B.O.C.C.)
7)	8.2.7.d(1)(b)	SIDEWALKS	08-29-05
8)	8.2.5.a(1)(d)		

CONSENT OF MORTGAGEE:

KNOW ALL MEN BY THESE PRESENTS: THAT COMPASS BANK, THE OWNER AND HOLDER OF THAT CERTAIN MORTGAGE DATED 01/17/06, AND RECORDED IN OFFICIAL RECORDS BOOK 4312, PAGE 1524 OF THE PUBLIC RECORDS OF MARION COUNTY, FLORIDA, ENCUMBERING THE PROPERTY HEREON, DOES CONSENT TO THIS PLAT AND JOINS IN THE ABOVE DEDICATION.

IN WITNESS WHEREOF SAID CORPORATION HAS CAUSED THESE PRESENTS TO BE SIGNED IN ITS CORPORATE NAME BY ITS CITY PRESIDENT ALL BY AND WITH THE AUTHORITY OF THE BOARD OF DIRECTORS OF SAID CORPORATION ON THIS 8 DAY OF JUNE, 2007.

COMPASS BANK

BY: R. J. Hilgenfeldt
ROY J. HILGENFELDT, CITY PRESIDENT

WITNESS: Brad Abbey
SIGNATURE

BRAD ABBEY
PRINTED NAME

WITNESS: Gay H. Baggert
SIGNATURE

Gay H. BAGGERT
PRINTED NAME

NOTARY ACKNOWLEDGMENT:

STATE OF FLORIDA
COUNTY OF MARION

BEFORE ME THIS DAY PERSONALLY APPEARED ROY J. HILGENFELDT, CITY PRESIDENT OF COMPASS BANK, TO ME WELL KNOWN TO BE THE PERSON DESCRIBED HEREIN OR WHO PRODUCED IDENTIFICATION AND ACKNOWLEDGED THAT HE DID SO AS AN OFFICER OF SAID CORPORATION ALL BY AND WITH THE AUTHORITY OF THE BOARD OF DIRECTORS OF SAID CORPORATION.

DATE: June 8, 2007

NOTARY PUBLIC Ch. H. Baggert
STATE OF FLORIDA AT LARGE

DEVELOPER'S ACKNOWLEDGMENT AND DEDICATION:

KNOW ALL MEN BY THESE PRESENTS: THAT AVONLEA, LLC., A FLORIDA LIMITED LIABILITY COMPANY HAS CAUSED TO BE MADE THE PLAT OF "AVONLEA PHASE 1", THE SAME BEING A SUBDIVISION OF LAND HEREON DESCRIBED AND THAT THE STREETS, AVENUES, ROADS, CIRCLES, LOOPS, AND PLACES AS SHOWN ON THIS PLAT TOGETHER WITH ALL IMPROVEMENTS THEREON SHALL BE PRIVATE PROPERTY AND ARE HEREBY DEDICATED TO AND MAINTAINED BY AVONLEA HOMEOWNERS ASSOCIATION, INC.; SUBJECT HOWEVER TO A PERPETUAL RIGHT OF EASEMENT HEREIN GRANTED FOR INGRESS AND EGRESS BY SANITATION, POSTAL, FIRE, LAW ENFORCEMENT, MEDICAL SERVICE VEHICLES AND THEIR PERSONNEL AND MARION COUNTY TRANSPORTATION PERSONNEL PROVIDING SERVICE TO THE SUBDIVISION AND THAT THE UTILITY EASEMENTS SHOWN OR NOTED ARE RESERVED EXCLUSIVELY FOR SUCH USES BY THE UTILITIES (MUNICIPAL, GOVERNMENTAL, AND PRIVATE), TO WHOM RIGHTS IN SUCH EASEMENTS SHALL BE GRANTED FROM TIME TO TIME BY THE DEDICATOR OR ITS SUCCESSORS IN INTEREST, AND THAT NO OTHER OBLIGATION IS IMPOSED UPON MARION COUNTY OR ANY OTHER PUBLIC BODY FOR IMPROVEMENT OR MAINTENANCE OF THE RIGHTS OF WAY, STORM WATER DRAINAGE FACILITIES OR EASEMENTS.

CONSERVATION EASEMENTS A THROUGH E ARE HEREBY DEDICATED TO ST. JOHNS RIVER WATER MANAGEMENT DISTRICT, PURSUANT TO SECTION 704.06, FLORIDA STATUTES, AND ARE TO BE MAINTAINED IN A NATURAL VEGETATIVE STATE AND FURTHER, THERE SHALL BE NO RIDING, DUMPING, LAND CLEARING, LIVESTOCK GRAZING, OR OTHER DISTURBANCE TO NATURAL SOILS OR VEGETATION WITHIN THE EASEMENTS.

TRACT A IS RESERVED AS A DRAINAGE RETENTION AREA AND IS HEREBY DEDICATED TO THE PUBLIC AND MAINTAINED BY MARION COUNTY.

TRACTS B AND C ARE RESERVED AS LANDSCAPE BUFFERS AND ARE HEREBY DEDICATED TO AND MAINTAINED BY AVONLEA HOMEOWNERS ASSOCIATION, INC.

TEN FOOT ADDITIONAL RIGHT OF WAY ALONG AND ADJACENT TO EAST HIGHWAY 25 IS HEREBY DEDICATED TO THE PUBLIC.

THE TWENTY FOOT EMERGENCY INGRESS/EGRESS EASEMENT AND CONSERVATION EASEMENT ACCESS IS HEREBY DEDICATED TO AND MAINTAINED BY AVONLEA HOMEOWNERS ASSOCIATION, INC. FOR SAID PURPOSES.

IN WITNESS WHEREOF AVONLEA, LLC, A FLORIDA LIMITED LIABILITY COMPANY, HAS CAUSED THESE PRESENTS TO BE SIGNED ON THIS 8 DAY OF JUNE, 2007.

AVONLEA, LLC

BY: Harvey Vandeven
HARVEY VANDEVEN, MANAGER

WITNESS: Diane Barrineau
SIGNATURE

DIANE BARRINEAU
PRINTED NAME

WITNESS: Seth Schneider
SIGNATURE

SETH SCHNEIDER
PRINTED NAME

NOTARY ACKNOWLEDGMENT:

STATE OF FLORIDA
COUNTY OF MARION

BEFORE ME THIS DAY PERSONALLY APPEARED, HARVEY VANDEVEN, AS MANAGER OF AVONLEA, LLC, A FLORIDA LIMITED LIABILITY COMPANY, TO ME WELL KNOWN TO BE THE PERSON DESCRIBED HEREIN OR WHO PRODUCED IDENTIFICATION AND WHO EXECUTED THE FOREGOING INSTRUMENT, AND WHO ACKNOWLEDGED THAT HE DID SO FREELY AND VOLUNTARILY FOR THE USES AND PURPOSES THEREIN EXPRESSED.

WITNESS MY HAND AND SEAL THIS 8 DAY OF JUNE, 2007.

NOTARY PUBLIC Diane L. Barrineau
STATE OF FLORIDA
COMMISSION EXPIRES:

DIANE L. BARRINEAU
MY COMMISSION # 00487690
EXPIRES: February 23, 2008
1400-3-NOTARY FL Notary Discount Assoc. Co.

SURVEYOR'S NOTES:

- THIS PLAT DEPICTS A SURVEY PERFORMED FOR THE SPECIFIC PURPOSE OF RECORDING A SUBDIVISION PLAT IN ACCORDANCE WITH THE PROVISIONS OF CHAPTER 177, FLORIDA STATUTES.
- BEARINGS ARE ASSUMED, BASED ON THE NORTHEASTERLY RIGHT OF WAY LINE OF E. HIGHWAY 25, AS BEING N.70°50'06"W.
- NO LOT SHALL BE DIVIDED OR RE-SUBDIVIDED EXCEPT FOR THE SOLE PURPOSE OF PROVIDING ADDITIONAL AREA TO ADJACENT LOTS OR UNTIL A REPLAT IS FILED WITH MARION COUNTY, WHICH REPLAT COMPLIES WITH THE PROVISIONS OF THE LAND DEVELOPMENT CODE, VIOLATION OF THIS PROVISION MAY BE PUNISHABLE AS PROVIDED IN THE CODE OF MARION COUNTY.
- ALL UTILITY EASEMENTS SHOWN HEREON SHALL ALSO BE EASEMENTS FOR THE CONSTRUCTION, INSTALLATION, MAINTENANCE, AND OPERATION OF CABLE TELEVISION SERVICES; PROVIDED, HOWEVER, NO SUCH CONSTRUCTION, INSTALLATION, MAINTENANCE AND OPERATION OF TELEVISION SERVICES SHALL INTERFERE WITH THE FACILITIES AND SERVICES OF AN ELECTRIC, TELEPHONE, GAS OR OTHER FACILITY.
- EASEMENTS ARE SHOWN BY DASHED LINES AND NOTED IN CHART ON THE ATTACHED PLAT. ALL PUBLIC UTILITY COMPANIES AND GOVERNMENTAL AGENCIES ARE GRANTED THE RIGHT TO INSTALL AND MAINTAIN UTILITIES AND DRAINAGE FACILITIES IN THE EASEMENTS.
- COUNTY OFFICIALS EMPLOYED BY THE COUNTY BUILDING AND ZONING DEPARTMENT, COUNTY ENVIRONMENTAL HEALTH DEPARTMENT, AND COUNTY ENGINEERING DEPARTMENT SHALL HAVE THE RIGHT TO ENTER UPON THE LANDS INCLUDED IN THIS PLAT FOR THE PURPOSES OF INSPECTING ANY AND ALL FACILITIES, STRUCTURES AND CONSTRUCTION OF IMPROVEMENTS IN ORDER TO ASSURE THAT THE SAME ARE IN KEEPING WITH THE PUBLIC SAFETY, HEALTH AND GENERAL WELFARE.
- STATE PLANE COORDINATES ARE BASED ON CITY OF OCALA ENGINEERING DEPARTMENT G.P.S. CONTROL POINT 0028 AND N.G.S. CONTROL POINT Q424, (NAD-83) 1990 ADJUSTMENT.
- THIS PLAT CONTAINS 30 LOTS, 3 TRACTS, AND 1.28 MILES OF ROAD.
- ALL DRIVEWAY ACCESS SHALL BE PROVIDED USING THE INTERNAL SUBDIVISION ROADWAYS CREATED WITH THIS SUBDIVISION. DIRECT ACCESS TO EAST HIGHWAY NO. 25 IS PROHIBITED.
- PROPOSED ROADS WILL BE PRIVATELY OWNED AND MAINTAINED BY AVONLEA HOMEOWNERS ASSOCIATION, INC.
- THIS PROPERTY IS IN A FLOOD ZONE "C" - AN AREA OF MINIMAL FLOODING AND FLOOD ZONE "A" - AN AREA OF 100-YEAR FLOOD AS PER THE NATIONAL FLOOD INSURANCE RATE MAP, COMMUNITY PANEL NO. 120160 0715 B, EFFECTIVE JANUARY 19, 1983.
- THIS SUBDIVISION LIES IN AN "ENVIRONMENTALLY SENSITIVE OVERLAY ZONE". THERE MAY BE ADDITIONAL REQUIREMENTS FOR BUILDING.
- ALL LOTS WILL BE SERVED BY INDIVIDUAL WELLS AND SEPTIC SYSTEMS. SEPTIC PERMITS TO BE CONSIDERED ON A LOT BY LOT BASIS.
- THIS SUBDIVISION PROJECT HAS BEEN ESTABLISHED UNDER THE "HAMLET" DEVELOPMENT PROVISIONS OF THE MARION COUNTY COMPREHENSIVE PLAN AND LAND DEVELOPMENT CODE (FLUE POLICY 3.1 AND LDC SECTION 8.3.3) IN EFFECT AT THE TIME OF THIS PROJECT'S REVIEW AND APPROVAL.
- EACH LOT MAY CONSTRUCT ONE DRIVEWAY CONNECTION IN A CORRIDOR 30' IN WIDTH. THE LOCATION OF THE DRIVEWAY SHALL BE DETERMINED AT THE TIME OF THE BUILDING PERMIT APPLICATION FOR EACH LOT.

SURVEYOR'S CERTIFICATE:

I HEREBY CERTIFY THAT THIS PLAT OF "AVONLEA PHASE 1" IS A TRUE AND CORRECT REPRESENTATION OF THE LAND AS RECENTLY SURVEYED AND PLATTED UNDER MY DIRECTION AND SUPERVISION; THAT THE PERMANENT REFERENCE MONUMENTS AS SHOWN HEREIN WERE IN PLACE ON THE 26TH OF APRIL, 2007; THAT PERMANENT CONTROL POINTS SHALL BE SET WITHIN ONE YEAR OF THE RECORDING OF THIS PLAT AND THAT THIS PLAT COMPLIES WITH THE REQUIREMENTS OF CHAPTER 177, FLORIDA STATUTES.

BY: Christopher J. Howson
CHRISTOPHER J. HOWSON, P.S.M.
FLORIDA REGISTERED SURVEYOR NO. LS 6553
R.M. BARRINEAU & ASSOCIATES, INC.
CERTIFICATE OF AUTHORIZATION NO. LB 5091
1309 S.E. 25TH LOOP, SUITE 103, OCALA, FLORIDA 34471

CLERK OF CIRCUIT COURT'S ACKNOWLEDGMENT:

I HEREBY CERTIFY THAT THE ATTACHED PLAT CONFORMS WITH THE PROVISIONS OF CHAPTER 177, FLORIDA STATUTES, AND THAT SAID PLAT WAS FILED FOR RECORD IN PLAT BOOK 10, AT PAGES 195-203 OF THE PUBLIC RECORDS OF MARION COUNTY, FLORIDA, AT 3:04 PM ON THIS 20th DAY OF JUNE, 2007.

BY: David R. Ellspermann
DAVID R. ELLSPERMANN
CLERK OF THE CIRCUIT COURT

ASSESSMENT NOTIFICATION:

THE BOARD OF COUNTY COMMISSIONERS OF MARION COUNTY, FLORIDA, AS A CONDITION PRECEDENT TO THIS PLAT FOR RECORDING IN THE PUBLIC RECORDS, DOES HEREBY NOTIFY ALL PRESENT AND FUTURE OWNERS OF PROPERTY SHOWN ON THIS PLAT THAT THE LANDS INCLUDED IN THIS PLAT ARE SUBJECT TO SPECIAL ASSESSMENTS AS MAY BE PERMITTED BY LAW TO FINANCE COSTS INCURRED IN CONNECTION WITH THE MAINTENANCE, OPERATION AND CONSTRUCTION OF A CENTRAL WATER SYSTEM AND SEWER SYSTEM AND/OR TRAFFIC SAFETY IMPROVEMENTS, INCLUDING, BUT NOT LIMITED TO TURN LANES, BY-PASS LANES AND TRAFFIC SIGNALS WHEN, IN THE OPINION OF SAID BOARD OR OTHER GOVERNING BODY HAVING JURISDICTION, SUCH FACILITIES BECOME NECESSARY IN ORDER TO PROTECT THE ENVIRONMENT AND THE HEALTH, SAFETY AND WELFARE OF THE GENERAL PUBLIC.


STAN MCCLAIN
CHAIRMAN
BOARD OF COUNTY COMMISSIONERS

PREPARED BY: R.M. BARRINEAU & ASSOCIATES, INC. 1309 S.E. 25TH LOOP, SUITE 103 OCALA, FLORIDA 34471
I HEREBY CERTIFY THAT I HAVE REVIEWED THIS PLAT FOR CONFORMITY WITH THE REQUIREMENTS OF CHAPTER 177, FLORIDA STATUTES, AS A PROFESSIONAL SURVEYOR AND MAPPER EMPLOYED BY MARION COUNTY.
JOHN R. ANCHER JR. P.S.M. 5531

AVONLEA PHASE 1

(A HAMLET SUBDIVISION)
SECTION 35, TOWNSHIP 16 SOUTH, RANGE 23 EAST &
SECTION 2, TOWNSHIP 17 SOUTH, RANGE 23 EAST,
MARION COUNTY, FLORIDA

PLAT BOOK 10, PAGE 196
SHEET 2 OF 9

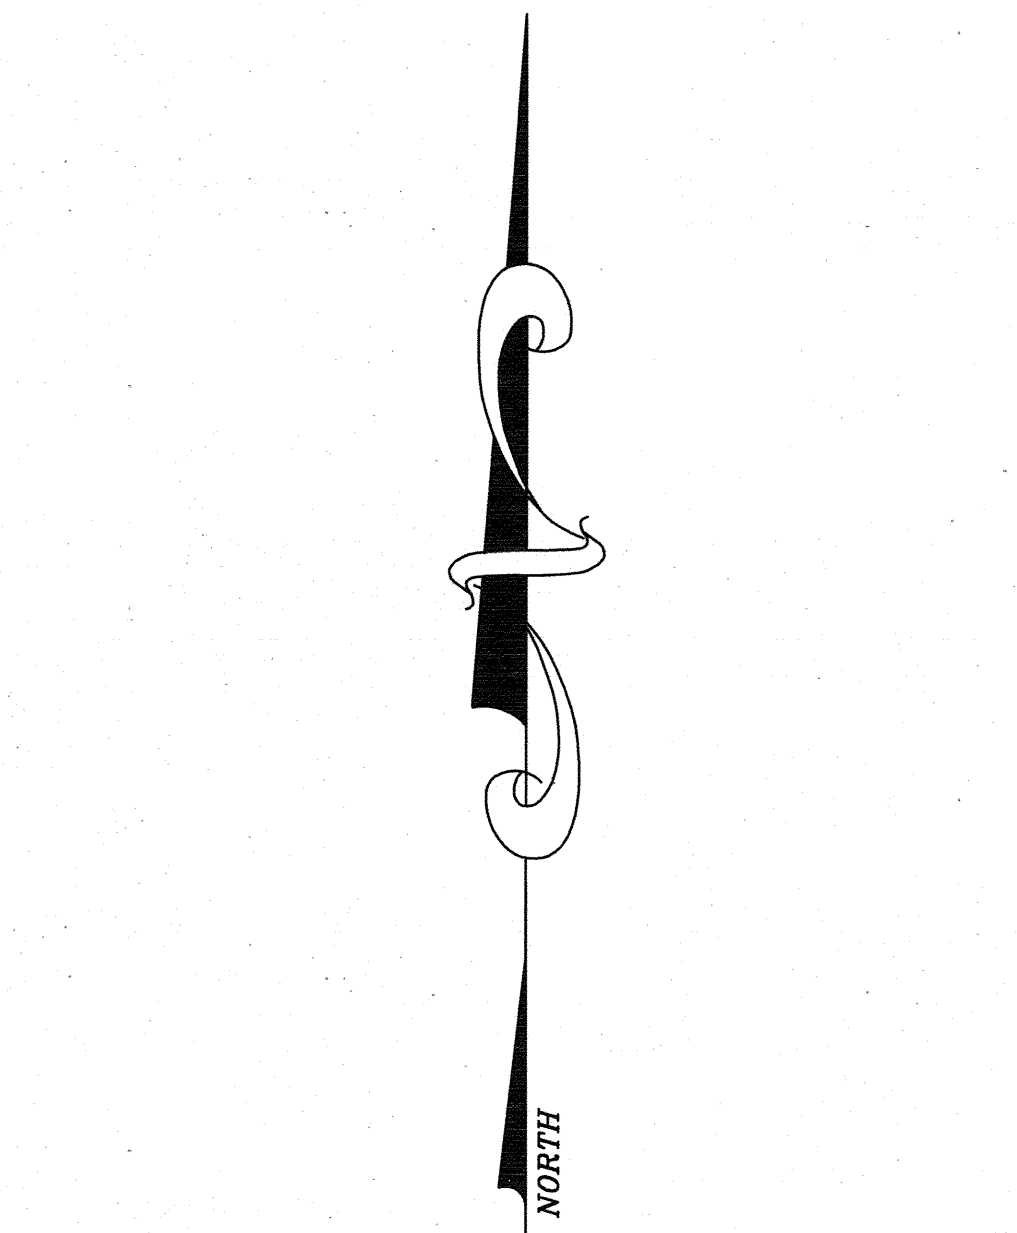


- LEGEND:** UNLESS OTHERWISE NOTED
- = PERMANENT REFERENCE MONUMENT SET 4"x4" CONCRETE MONUMENT NO LB5091
 - = PERMANENT REFERENCE MONUMENT FOUND 4"x4" CONCRETE MONUMENT I.D. - MOOREHEAD ENGINEERING COMPANY
 - = PERMANENT CONTROL POINT SET NAIL & DISK I.D. - LB5091
 - R/W = RIGHT-OF-WAY
 - (NR) = NON-RADIAL
 - = CENTERLINE OF RIGHT OF WAY
 - - - = BREAKLINE NOT TO SCALE
 - O.R. = OFFICIAL RECORDS
 - P.R.C. = POINT OF REVERSE CURVATURE
 - P.C. = POINT OF CURVATURE
 - P.T. = POINT OF TANGENCY
 - I.D. = IDENTIFICATION
 - (R) = RADIAL LINE
 - (TYP) = TYPICAL
 - D.E. = DRAINAGE EASEMENT
 - L.B. = LANDSCAPE BUFFER
 - U.E. = UTILITY EASEMENT
 - D.R.A. = DRAINAGE RETENTION AREA
 - = DRIVEWAY PROHIBITED WITHIN THIS AREA
 - = CENTERLINE OF RIGHT OF WAY
 - = DENOTES BUILDABLE AREA
 - = DENOTES MEANDER LINE

NOTE:
10' UTILITY EASEMENT RESERVED ALONG AND ADJACENT TO RIGHTS-OF-WAYS

R.M. BARRINEAU & ASSOCIATES, INC.

PROFESSIONAL SURVEYORS & MAPPERS

1309 S.E. 25TH LOOP, SUITE 103
OCALA, FLORIDA 34471
PHONE (352) 622-3133
FAX (352) 369-3771
REGINALD M. BARRINEAU, P.S.M. - FOUNDER
CERTIFICATE OF AUTHORIZATION NO. LB 5091
KEVIN J. PLANAGAN, P.S.M. - LS 3942
CHRISTOPHER J. HOWSON, P.S.M. - LS 6553
MELVIN A. BOWEN, P.S.M. - LS 5035

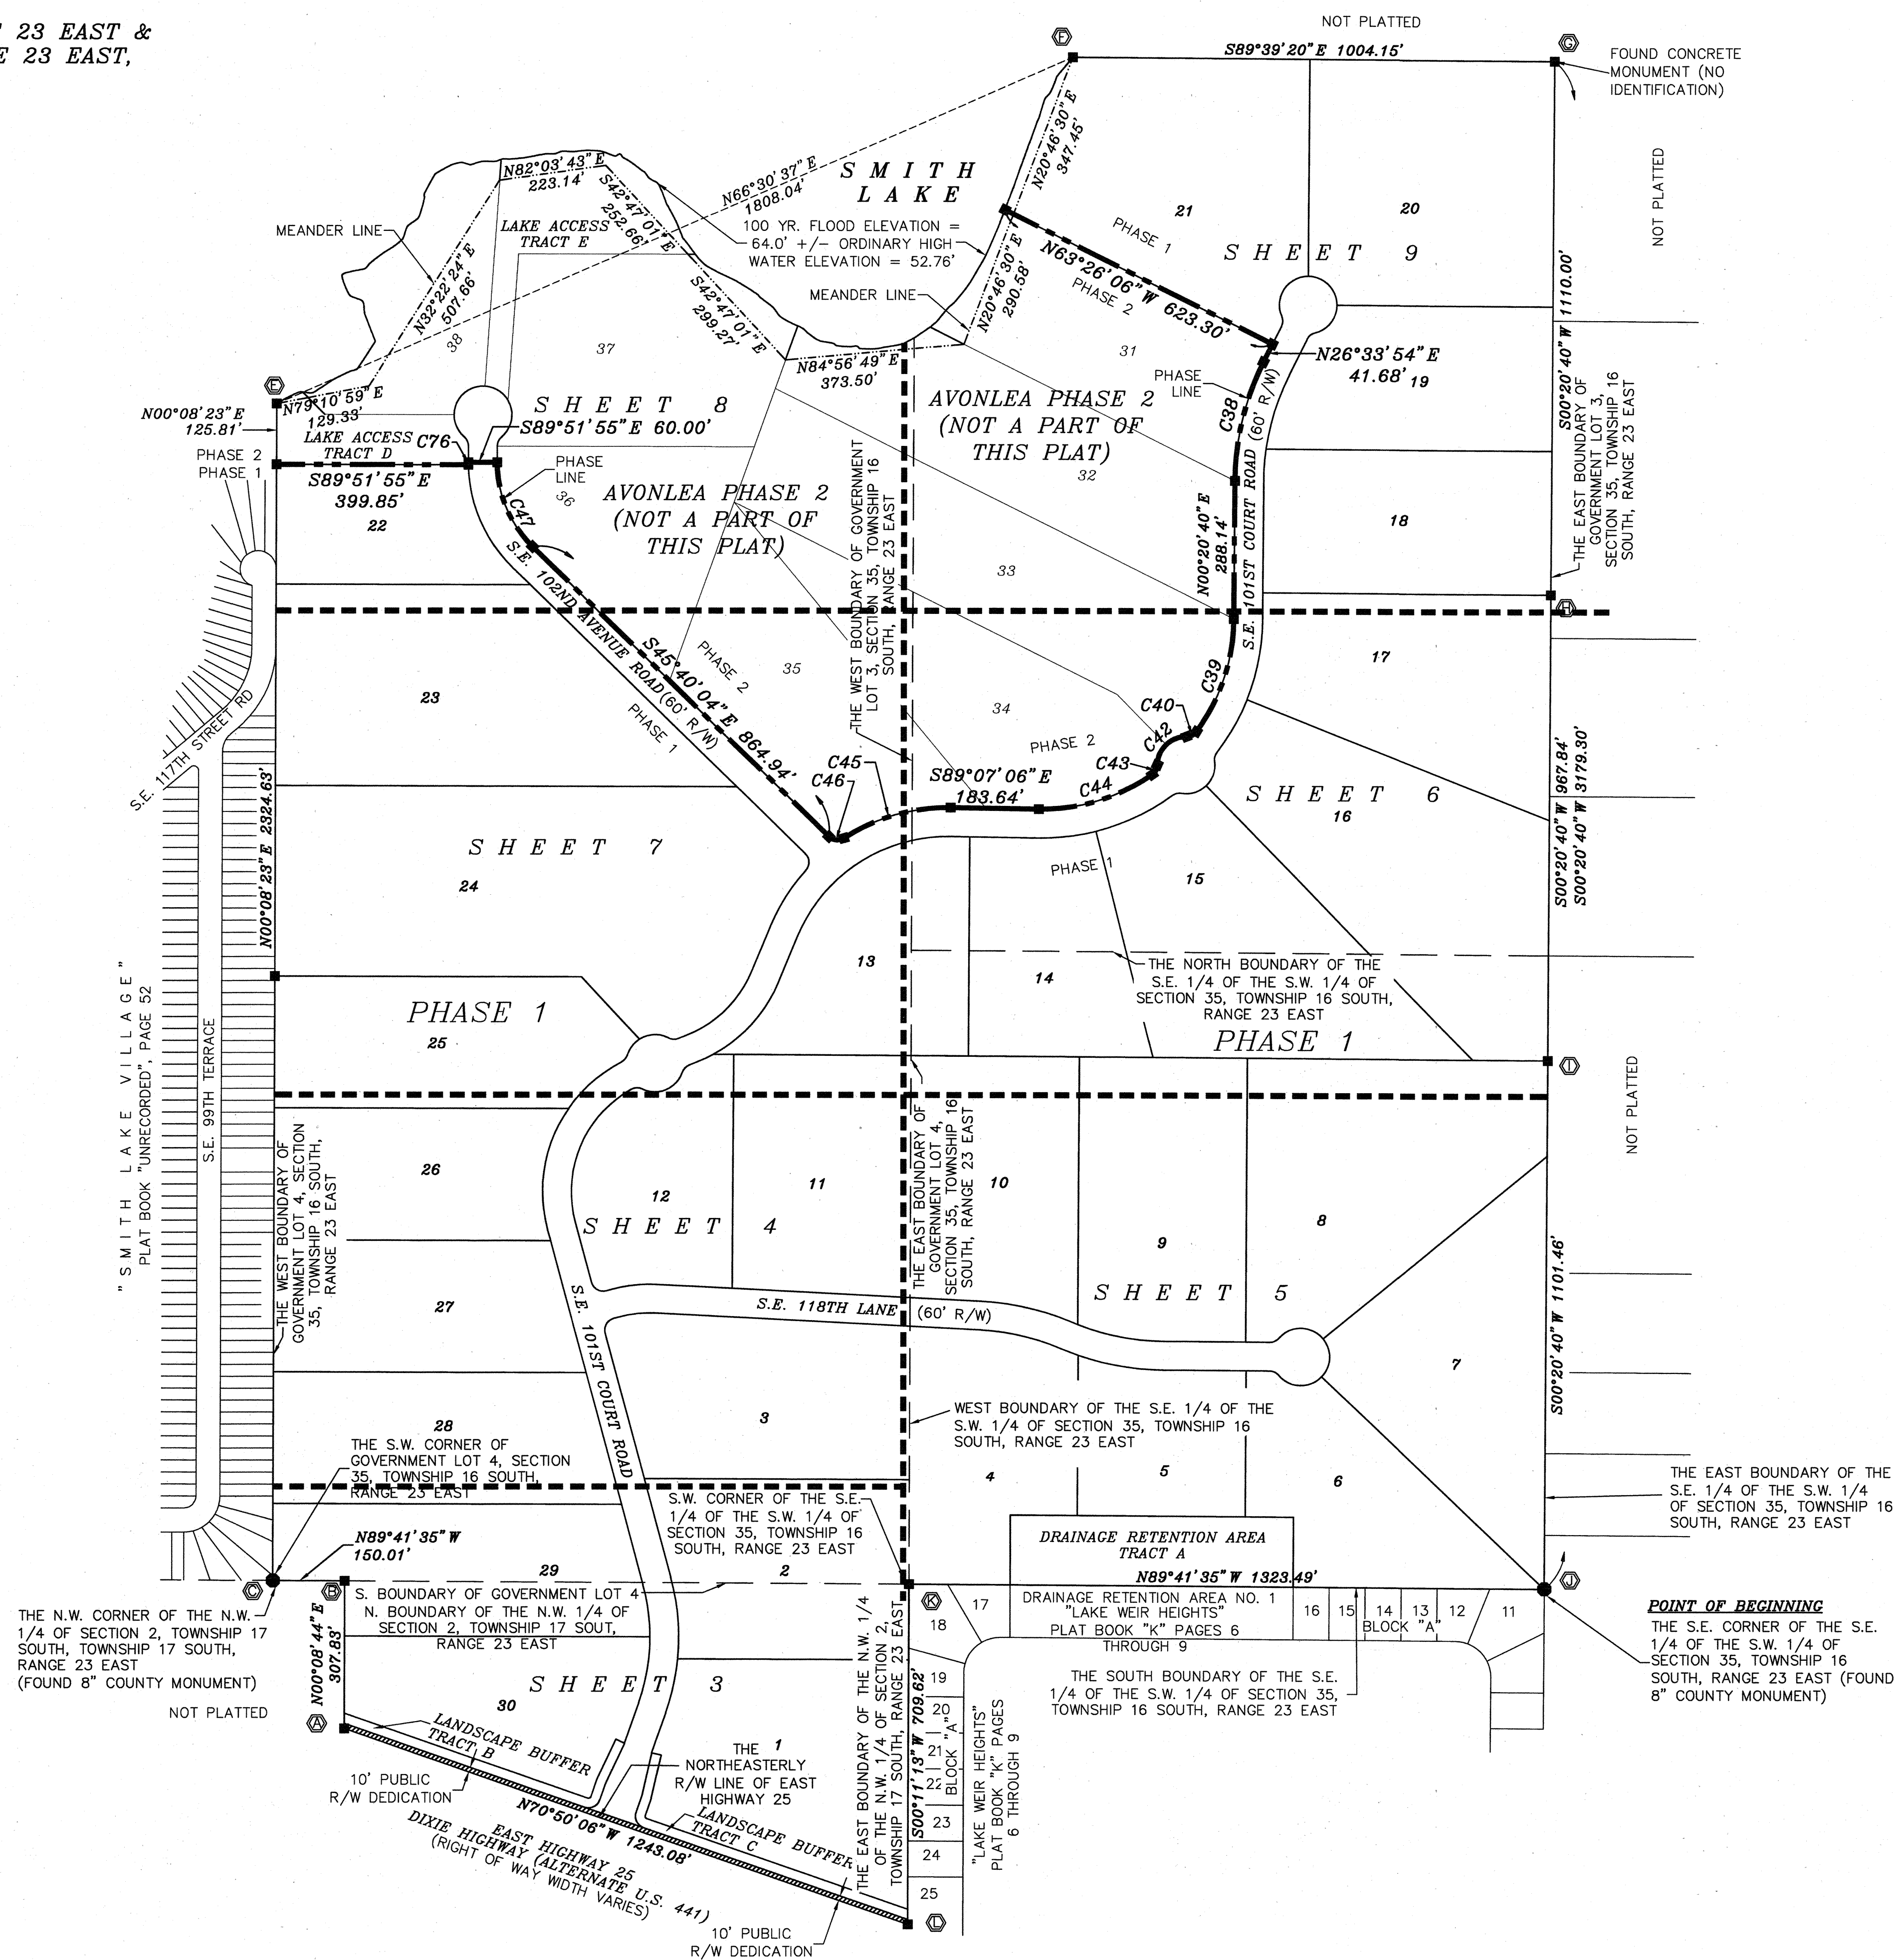

CURVE TABLE				
CURVE	DELTA	RADIUS	ARC	CHORD
C1	90°00'00"	25.00'	39.27'	35.36'
C2	13°42'56"	480.00'	114.90'	114.63'
C3	20°30'05"	480.00'	171.75'	170.84'
C4	90°00'00"	25.00'	39.27'	35.36'
C5	17°52'18"	245.00'	76.78'	76.46'
C6	20°02'43"	500.00'	174.93'	174.04'
C7	4°00'54"	560.00'	39.24'	39.23'
C8	18°37'34"	560.00'	182.05'	181.25'
C9	49°40'47"	25.00'	21.68'	21.00'
C10	96°23'52"	60.00'	100.95'	89.46'
C11	82°50'13"	60.00'	86.75'	79.39'
C12	100°07'29"	60.00'	104.85'	92.01'
C13	49°40'47"	25.00'	21.68'	21.00'
C14	21°07'11"	500.00'	184.30'	183.26'
C15	1°31'17"	500.00'	13.28'	13.28'
C16	20°02'43"	560.00'	195.92'	194.92'
C17	17°52'18"	305.00'	95.58'	95.19'
C18	90°00'00"	25.00'	39.27'	35.36'
C19	97°33'16"	60.00'	102.16'	90.26'
C20	6°48'23"	305.00'	36.23'	36.21'
C21	38°41'42"	305.00'	205.98'	202.09'
C22	68°12'26"	340.00'	404.75'	381.27'
C23	15°06'36"	460.00'	121.31'	120.96'
C24	22°01'15"	460.00'	176.79'	175.71'
C25	45°44'00"	25.00'	19.95'	19.43'
C26	53°52'16"	60.00'	56.41'	54.36'
C27	53°52'16"	60.00'	56.41'	54.36'
C28	45°44'00"	25.00'	19.95'	19.43'
C29	15°46'14"	460.00'	126.61'	126.22'
C30	21°21'37"	460.00'	171.49'	170.50'
C31	7°42'39"	500.00'	67.29'	67.24'
C32	18°30'36"	500.00'	161.53'	160.83'
C33	49°40'47"	25.00'	21.68'	21.00'
C34	75°54'02"	60.00'	79.48'	73.80'
C35	89°59'59"	60.00'	94.25'	84.85'
C36	113°27'33"	60.00'	118.81'	100.33'
C37	49°40'47"	25.00'	21.68'	21.00'
C38	26°13'14"	560.00'	256.28'	254.05'
C39	36°00'42"	400.00'	251.41'	247.29'
C40	54°28'00"	25.00'	23.77'	22.88'
C41	90°25'10"	60.00'	94.69'	85.16'
C42	54°28'00"	25.00'	23.77'	22.88'
C43	36°00'42"	400.00'	251.41'	247.29'
C44	33°38'30"	400.00'	234.86'	231.50'
C45	77°05'32"	25.00'	33.64'	31.16'
C46	45°48'09"	245.00'	195.85'	190.68'
C47	49°40'47"	25.00'	21.68'	21.00'
C48	79°22'03"	60.00'	83.11'	76.63'
C49	56°26'34"	60.00'	59.11'	56.75'
C50	93°52'10"	60.00'	98.30'	87.67'
C51	49°40'47"	60.00'	52.02'	50.41'
C52	49°40'47"	25.00'	21.68'	21.00'
C53	44°47'38"	305.00'	238.45'	232.42'
C54	87°58'08"	25.00'	38.38'	34.72'
C55	19°37'37"	400.00'	137.02'	136.35'
C56	45°30'05"	245.00'	194.57'	189.49'
C57	40°19'57"	60.00'	42.24'	41.37'
C58	49°37'19"	305.00'	264.15'	255.97'
C59	14°57'25"	420.00'	109.64'	109.33'
C60	19°15'36"	420.00'	141.18'	140.52'
C61	90°00'00"	25.00'	39.27'	35.36'
C62	93°14'28"	20.16'	32.81'	29.31'
C63	89°17'37"	19.16'	29.86'	26.93'
C64	84°03'41"	19.97'	29.30'	26.74'
C65	77°45'23"	21.00'	28.50'	26.36'
C66	90°00'45"	21.00'	32.99'	29.70'
C67	17°54'05"	188.32'	58.84'	58.60'
C68	16°20'00"	188.32'	53.68'	53.50'
C69	126°33'05"	16.00'	35.34'	28.58'
C70	108°15'50"	31.00'	58.58'	50.24'
C71	54°48'55"	50.00'	47.84'	46.03'
C72	115°22'15"	26.00'	52.35'	43.95'
C73	32°42'35"	50.00'	28.54'	28.16'
C74	102°09'08"	25.00'	44.57'	38.90'
C75	1°00'31"	305.00'	5.37'	5.37'
C76	45°24'13"	25.00'	19.81'	19.30'
C77	55°38'01"	25.00'	24.27'	23.33'
C78	49°40'47"	25.00'	21.68'	21.00'
C79	49°40'47"	25.00'	21.68'	21.00'
C80	75°28'08"	245.00'	322.71'	299.88'
C81	27°53'53"	305.00'	148.51'	147.05'
C82	60°27'30"	60.00'	63.31'	60.42'
C83				
C84				

STATE PLANE COORDINATES:

POINT	NORTHING	EASTING	SCALE FACTOR
Q424	1689706.2443	660315.3325	0.999941196
COED 0028	1734962.9634	639104.6136	0.999941510
A	1713346.1737	660396.5679	0.999941197
B	1713654.0010	660396.8496	0.999941197
C	1713654.5607	660246.8371	0.999941196
D	1714914.1935	660247.8597	0.999941196
E	1716105.0015	660248.8244	0.999941196
F	1716828.3502	661905.8583	0.999941216
G	1716823.9443	662909.9979	0.999941229
H	1715713.9567	662905.1314	0.999941229
I	1714746.1303	662900.8882	0.999941228
J	1713644.6759	662896.0591	0.999941228
K	1713649.6141	661572.5766	0.999941210
L	1712939.9934	661571.4147	0.999941210

(A HAMLET SUBDIVISION)
SECTION 35, TOWNSHIP 16 SOUTH, RANGE 23 EAST &
SECTION 2, TOWNSHIP 17 SOUTH, RANGE 23 EAST,
MARION COUNTY, FLORIDA

(A HAMLET SUBDIVISION)

SECTION 35, TOWNSHIP 16 SOUTH, RANGE 23 EAST &
SECTION 2, TOWNSHIP 17 SOUTH, RANGE 23 EAST,
MARION COUNTY, FLORIDA



MARION COUNTY, FLORIDA

LEGEND: UNLESS OTHERWISE NOTED

- | | | | |
|---|--------------------------------|--------|--|
| ■ | = PERMANENT REFERENCE MONUMENT | O.R. | = OFFICIAL RECORDS |
| SET 4"x4" CONCRETE MONUMENT NO LB5091 | | P.R.C. | = POINT OF REVERSE CURVATURE |
| □ | = PERMANENT REFERENCE MONUMENT | P.C. | = POINT OF CURVATURE |
| FOUND 4"x4" CONCRETE MONUMENT | | P.T. | = POINT OF TANGENCY |
| I.D. - MOOREHEAD ENGINEERING COMPANY | | I.D. | = IDENTIFICATION |
| ● | = PERMANENT CONTROL POINT | (R) | = RADIAL LINE |
| SET NAIL & DISK I.D. - LB5091 | | (TYP) | = TYPICAL |
| R/W | = RIGHT-OF-WAY | D.E. | = DRAINAGE EASEMENT |
| (NR) | = NON-RADIAL | L.B. | = LANDSCAPE BUFFER |
| —C— | = CENTERLINE OF RIGHT OF WAY | U.E. | = UTILITY EASEMENT |
| —V— | = BREAKLINE NOT TO SCALE | D.R.A. | = DRAINAGE RETENTION AREA |
|  | = DENOTES BUILDABLE AREA | — | = DRIVEWAY PROHIBITED WITHIN THIS AREA |
| — | = DENOTES MEANDER LINE | | |

O.R. = OFFICIAL RECORDS
P.R.C. = POINT OF REVERSE CURVATURE
P.C. = POINT OF CURVATURE
P.T. = POINT OF TANGENCY
I.D. = IDENTIFICATION
(R) = RADIAL LINE
(TYP) = TYPICAL
D.E. = DRAINAGE EASEMENT
L.B. = LANDSCAPE BUFFER
U.E. = UTILITY EASEMENT
D.R.A. = DRAINAGE RETENTION AREA
— = DRIVEWAY PROHIBITED WITHIN T

D.R.A. = DRAINAGE RETENTION AREA
 — = DRIVEWAY PROHIBITED WITHIN THIS AREA

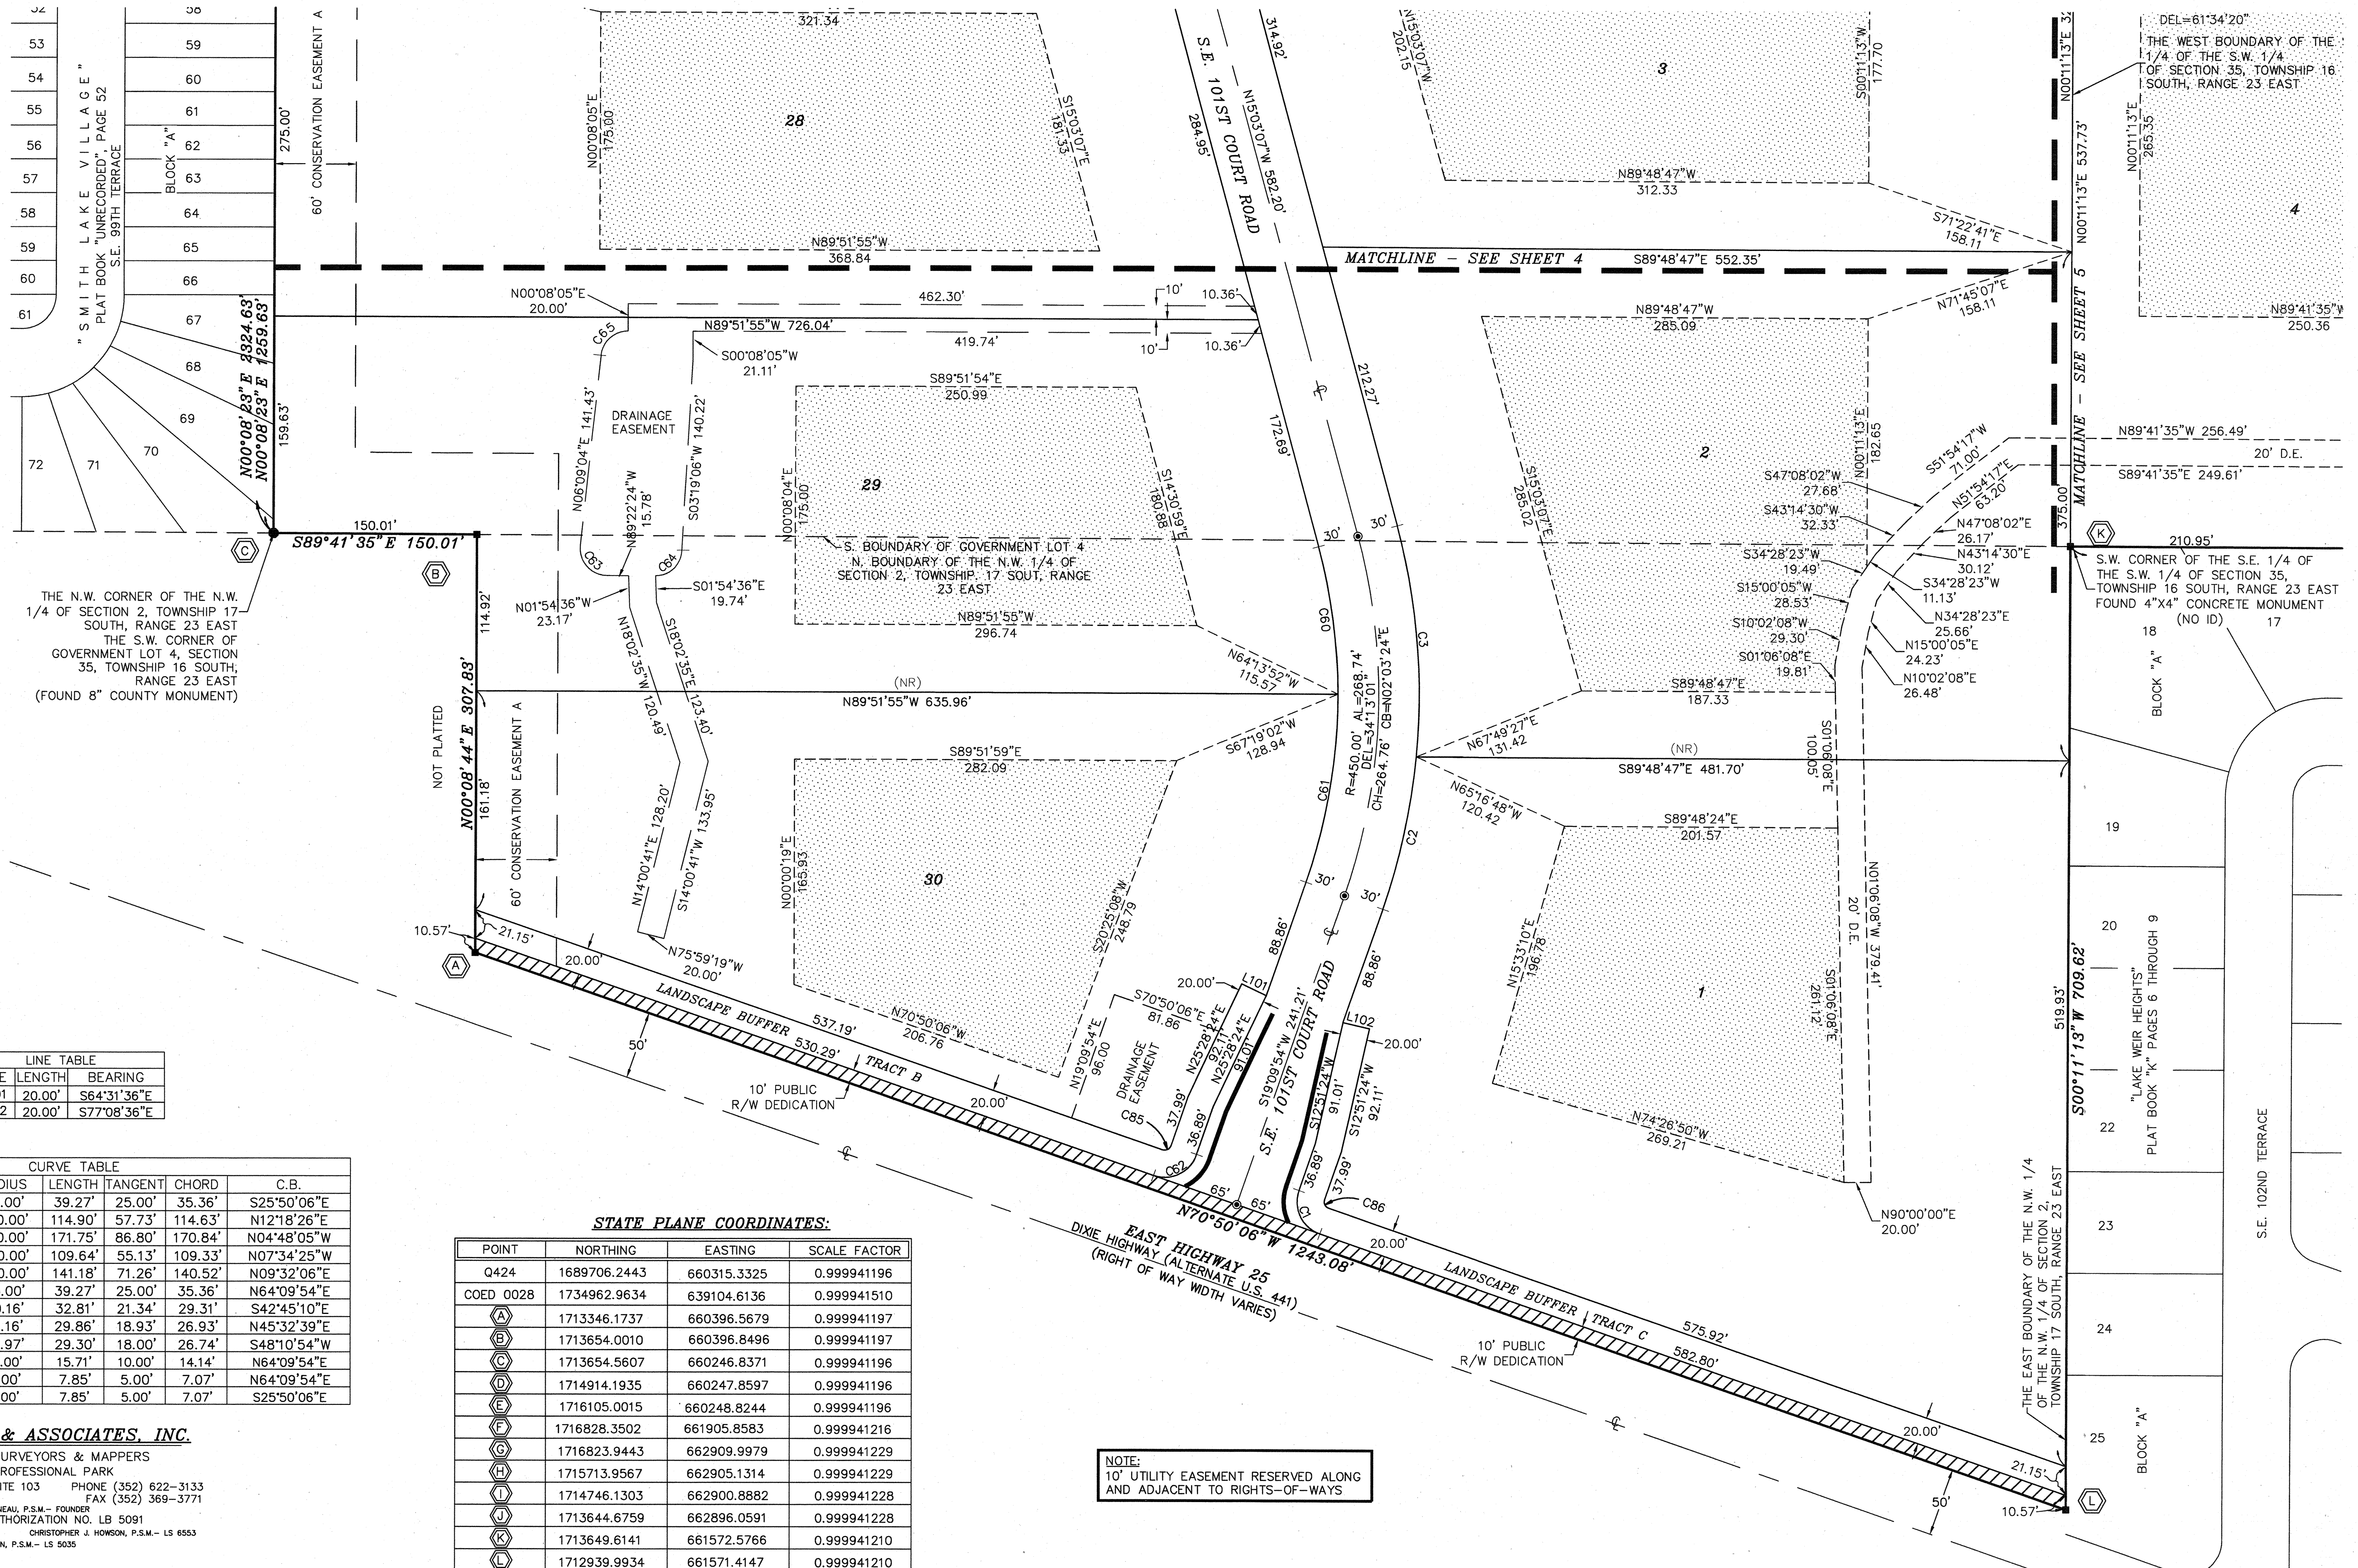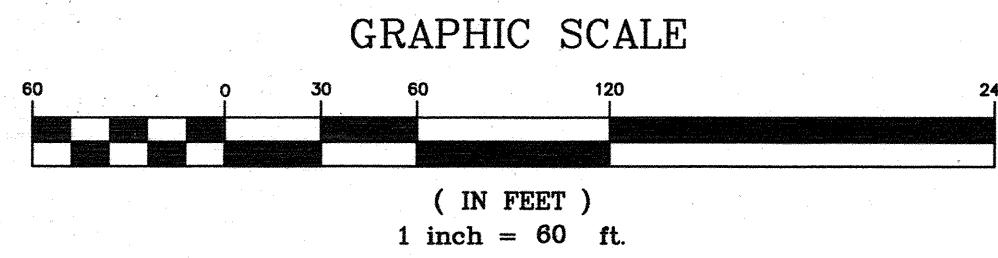

LINE TABLE		
LINE	LENGTH	BEARING
L101	20.00'	S64°31'36"E
L102	20.00'	S77°08'36"E

CURVE TABLE						
NO.	DELTA	RADIUS	LENGTH	TANGENT	CHORD	C.B.
C1	90°00'00"	25.00'	39.27'	25.00'	35.36'	S25°50'06"E
C2	13°42'56"	480.00'	114.90'	57.73'	114.63'	N12°18'26"E
C3	20°30'05"	480.00'	171.75'	86.80'	170.84'	N04°48'05"W
C60	14°57'25"	420.00'	109.64'	55.13'	109.33'	N07°34'25"W
C61	19°15'36"	420.00'	141.18'	71.26'	140.52'	N09°32'06"E
C62	90°00'00"	25.00'	39.27'	25.00'	35.36'	N64°09'54"E
C63	93°14'28"	20.16'	32.81'	21.34'	29.31'	S42°45'10"E
C64	89°17'37"	19.16'	29.86'	18.93'	26.93'	N45°32'39"E
C65	84°03'41"	19.97'	29.30'	18.00'	26.74'	S48°10'54"W
C77	90°00'00"	10.00'	15.71'	10.00'	14.14'	N64°09'54"E
C85	90°00'00"	5.00'	7.85'	5.00'	7.07'	N64°09'54"E
C86	90°00'00"	5.00'	7.85'	5.00'	7.07'	S25°50'06"E

STATE PLANE COORDINATES:

POINT	NORTHING	EASTING	SCALE FACTOR
Q424	1689706.2443	660315.3325	0.999941150
COED 0028	1734962.9634	639104.6136	0.999941196
(A)	1713346.1737	660396.5679	0.999941197
(B)	1713654.0010	660396.8496	0.999941197
(C)	1713654.5607	660246.8371	0.999941196
(D)	1714914.1935	660247.8597	0.999941196
(E)	1716105.0015	660248.8244	0.999941196
(F)	1716828.3502	661905.8583	0.999941216
(G)	1716823.9443	662909.9979	0.999941229
(H)	1715713.9567	662905.1314	0.999941228
(I)	1714746.1303	662900.8882	0.999941229
(J)	1713644.6759	662896.0591	0.999941228
(K)	1713649.6141	661572.5766	0.999941210
(L)	1712939.9934	661571.4147	0.999941210

NOTE:
10' UTILITY EASEMENT RESERVED ALONG
AND ADJACENT TO RIGHTS-OF-WAYS

R.M. BARRINEAU & ASSOCIATES, INC

PROFESSIONAL SURVEYORS & MAPPERS
OAKHURST PROFESSIONAL PARK
9 S.E. 25TH LOOP, SUITE 103 PHONE (352) 622-3133
LA, FLORIDA 34471 FAX (352) 369-3771
REGINALD M. BARRINEAU, P.S.M. - FOUNDER
CERTIFICATE OF AUTHORIZATION NO. LB 5091
PLANAGAN, P.S.M. - LS 3942 CHRISTOPHER J. HOWSON, P.S.M. - LS 6553
MELVIN A. BOWEN, P.S.M. - LS 5035


KEVIN J. FLANAGAN, P.S.M.- LS 3942 CHRISTOPHER J. HOWSON, P.S.M.- LS 6553
MELVIN A. BOWEN, P.S.M.- LS 5035

PREPARED BY: R.M. BARRINEAU & ASSOCIATES, INC. 1309 S.E. 25TH LOOP, SUITE 103 OCALA, FLORIDA 34471


AVONLEA PHASE 1

(A HAMLET SUBDIVISION)
SECTION 35, TOWNSHIP 16 SOUTH, RANGE 23 EAST &
SECTION 2, TOWNSHIP 17 SOUTH, RANGE 23 EAST,
MARION COUNTY, FLORIDA

GRAPHIC SCALE

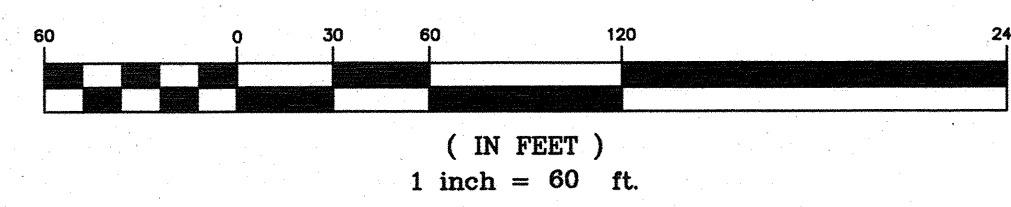

NOTE:
10' UTILITY EASEMENT RESERVED ALONG
AND ADJACENT TO RIGHTS-OF-WAYS

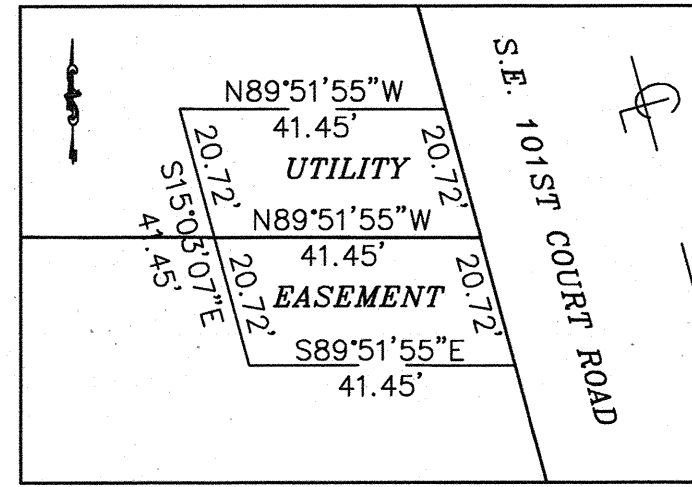

DETAIL C
1"=30'

CURVE TABLE					
NO.	DELTA	RADIUS	LENGTH	TANGENT	CHORD
C4	90°00'00"	25.00'	39.27'	25.00'	35.36'
C5	17°57'18"	245.00'	76.78'	38.71'	76.46'
C6	20°02'43"	500.00'	174.93'	88.37'	174.04'
C7	4°00'54"	560.00'	39.24'	19.63'	39.23'
C8	18°37'34"	560.00'	182.05'	91.83'	181.25'
C9	49°40'47"	25.00'	21.68'	11.57'	21.00'
C10	96°23'52"	60.00'	100.95'	67.10'	89.46'
C11	82°50'13"	60.00'	86.75'	52.93'	79.39'
C12	100°07'29"	60.00'	104.85'	71.66'	92.01'
C13	49°40'47"	25.00'	21.68'	11.57'	21.00'
C14	21°07'11"	500.00'	184.30'	93.21'	183.26'
C15	1°31'17"	500.00'	13.28'	6.64'	13.28'
C16	20°02'43"	560.00'	195.92'	98.97'	194.92'
C17	17°57'18"	305.00'	95.58'	48.18'	95.19'
C18	90°00'00"	25.00'	39.27'	25.00'	35.36'
C19	97°33'16"	60.00'	102.16'	68.48'	90.26'
C20	6°48'23"	305.00'	36.23'	18.14'	36.21'
C21	38°41'42"	305.00'	205.98'	107.09'	202.09'
C57	45°30'05"	245.00'	194.57'	102.74'	189.49'
C58	40°19'57"	60.00'	42.24'	22.04'	41.37'
C59	49°37'19"	305.00'	264.15'	141.00'	255.97'
C65	84°03'41"	19.97'	29.30'	18.00'	26.74'
C78	45°24'13"	25.00'	19.81'	10.46'	19.30'
C79	55°38'01"	25.00'	24.27'	13.19'	23.33'
C80	49°40'47"	25.00'	21.68'	11.57'	21.00'
C81	49°40'47"	25.00'	21.68'	11.57'	21.00'
C82	75°28'08"	245.00'	322.71'	189.59'	299.88'
C83	27°53'53"	305.00'	148.51'	75.76'	147.05'
C84	60°27'30"	60.00'	63.31'	34.96'	60.42'

STATE PLANE COORDINATES:

POINT	NORTHING	EASTING	SCALE FACTOR
Q424	1689706.2443	660315.3325	0.999941196
COED 0028	1734962.9634	639104.6136	0.999941510
(A)	1713346.1737	660396.5679	0.999941197
(B)	1713654.0010	660396.8496	0.999941197
(C)	1713654.5607	660246.8371	0.999941196
(D)	1714914.1935	660247.8597	0.999941196
(E)	1716105.0015	660248.8244	0.999941196
(F)	1716828.3502	661905.8583	0.999941216
(G)	1716823.9443	662909.9979	0.999941229
(H)	1715713.9567	662905.1314	0.999941229
(I)	1714746.1303	662900.8882	0.999941228
(J)	1713644.6759	662896.0591	0.999941228
(K)	1713649.6141	661572.5766	0.999941210
(L)	1712939.9934	661571.4147	0.999941210

R.M. BARRINEAU & ASSOCIATES, INC.


PROFESSIONAL SURVEYORS & MAPPERS
OAKHURST PROFESSIONAL PARK
1309 S.E. 25TH LOOP, SUITE 103, Ocala, Florida 34471
PHONE (352) 622-3133 FAX (352) 369-3771
REGINALD W. BARRINEAU, P.S.M. - FOUNDER
CERTIFICATE OF AUTHORIZATION NO. LB 5091
KEVIN J. FLANAGAN, P.S.M. - LS 3942
CHRISTOPHER J. HOWSON, P.S.M. - LS 6553
MELVIN A. BOWEN, P.S.M. - LS 5035

LEGEND: UNLESS OTHERWISE NOTED

- PERMANENT REFERENCE MONUMENT SET 4"x4" CONCRETE MONUMENT NO LB5091
- PERMANENT REFERENCE MONUMENT FOUND 4"x4" CONCRETE MONUMENT I.D. - MOOREHEAD ENGINEERING COMPANY
- PERMANENT CONTROL POINT SET NAIL & DISK I.D. - LB5091
- RIGHT-OF-WAY
- NON-RADIAL
- CENTERLINE OF RIGHT OF WAY
- BREAKLINE NOT TO SCALE
- DENOTES BUILDABLE AREA
- DENOTES MEANDER LINE
- OFFICIAL RECORDS
- POINT OF REVERSE CURVATURE
- POINT OF CURVATURE
- POINT OF TANGENCY
- IDENTIFICATION
- RADIAL LINE
- TYPICAL
- DRAINAGE EASEMENT
- UTILITY EASEMENT
- DRAINAGE RETENTION AREA
- DRIVEWAY PROHIBITED WITHIN THIS AREA
- LANDSCAPE BUFFER

PLAT BOOK 10, PAGE 198
SHEET 4 OF 9

LINE TABLE		
LINE	LENGTH	BEARING
L44	50.00'	S52°55'32"W
L45	50.00'	S76°26'40"W
L46	50.00'	N63°58'55"W
L47	50.00'	N48°39'56"W

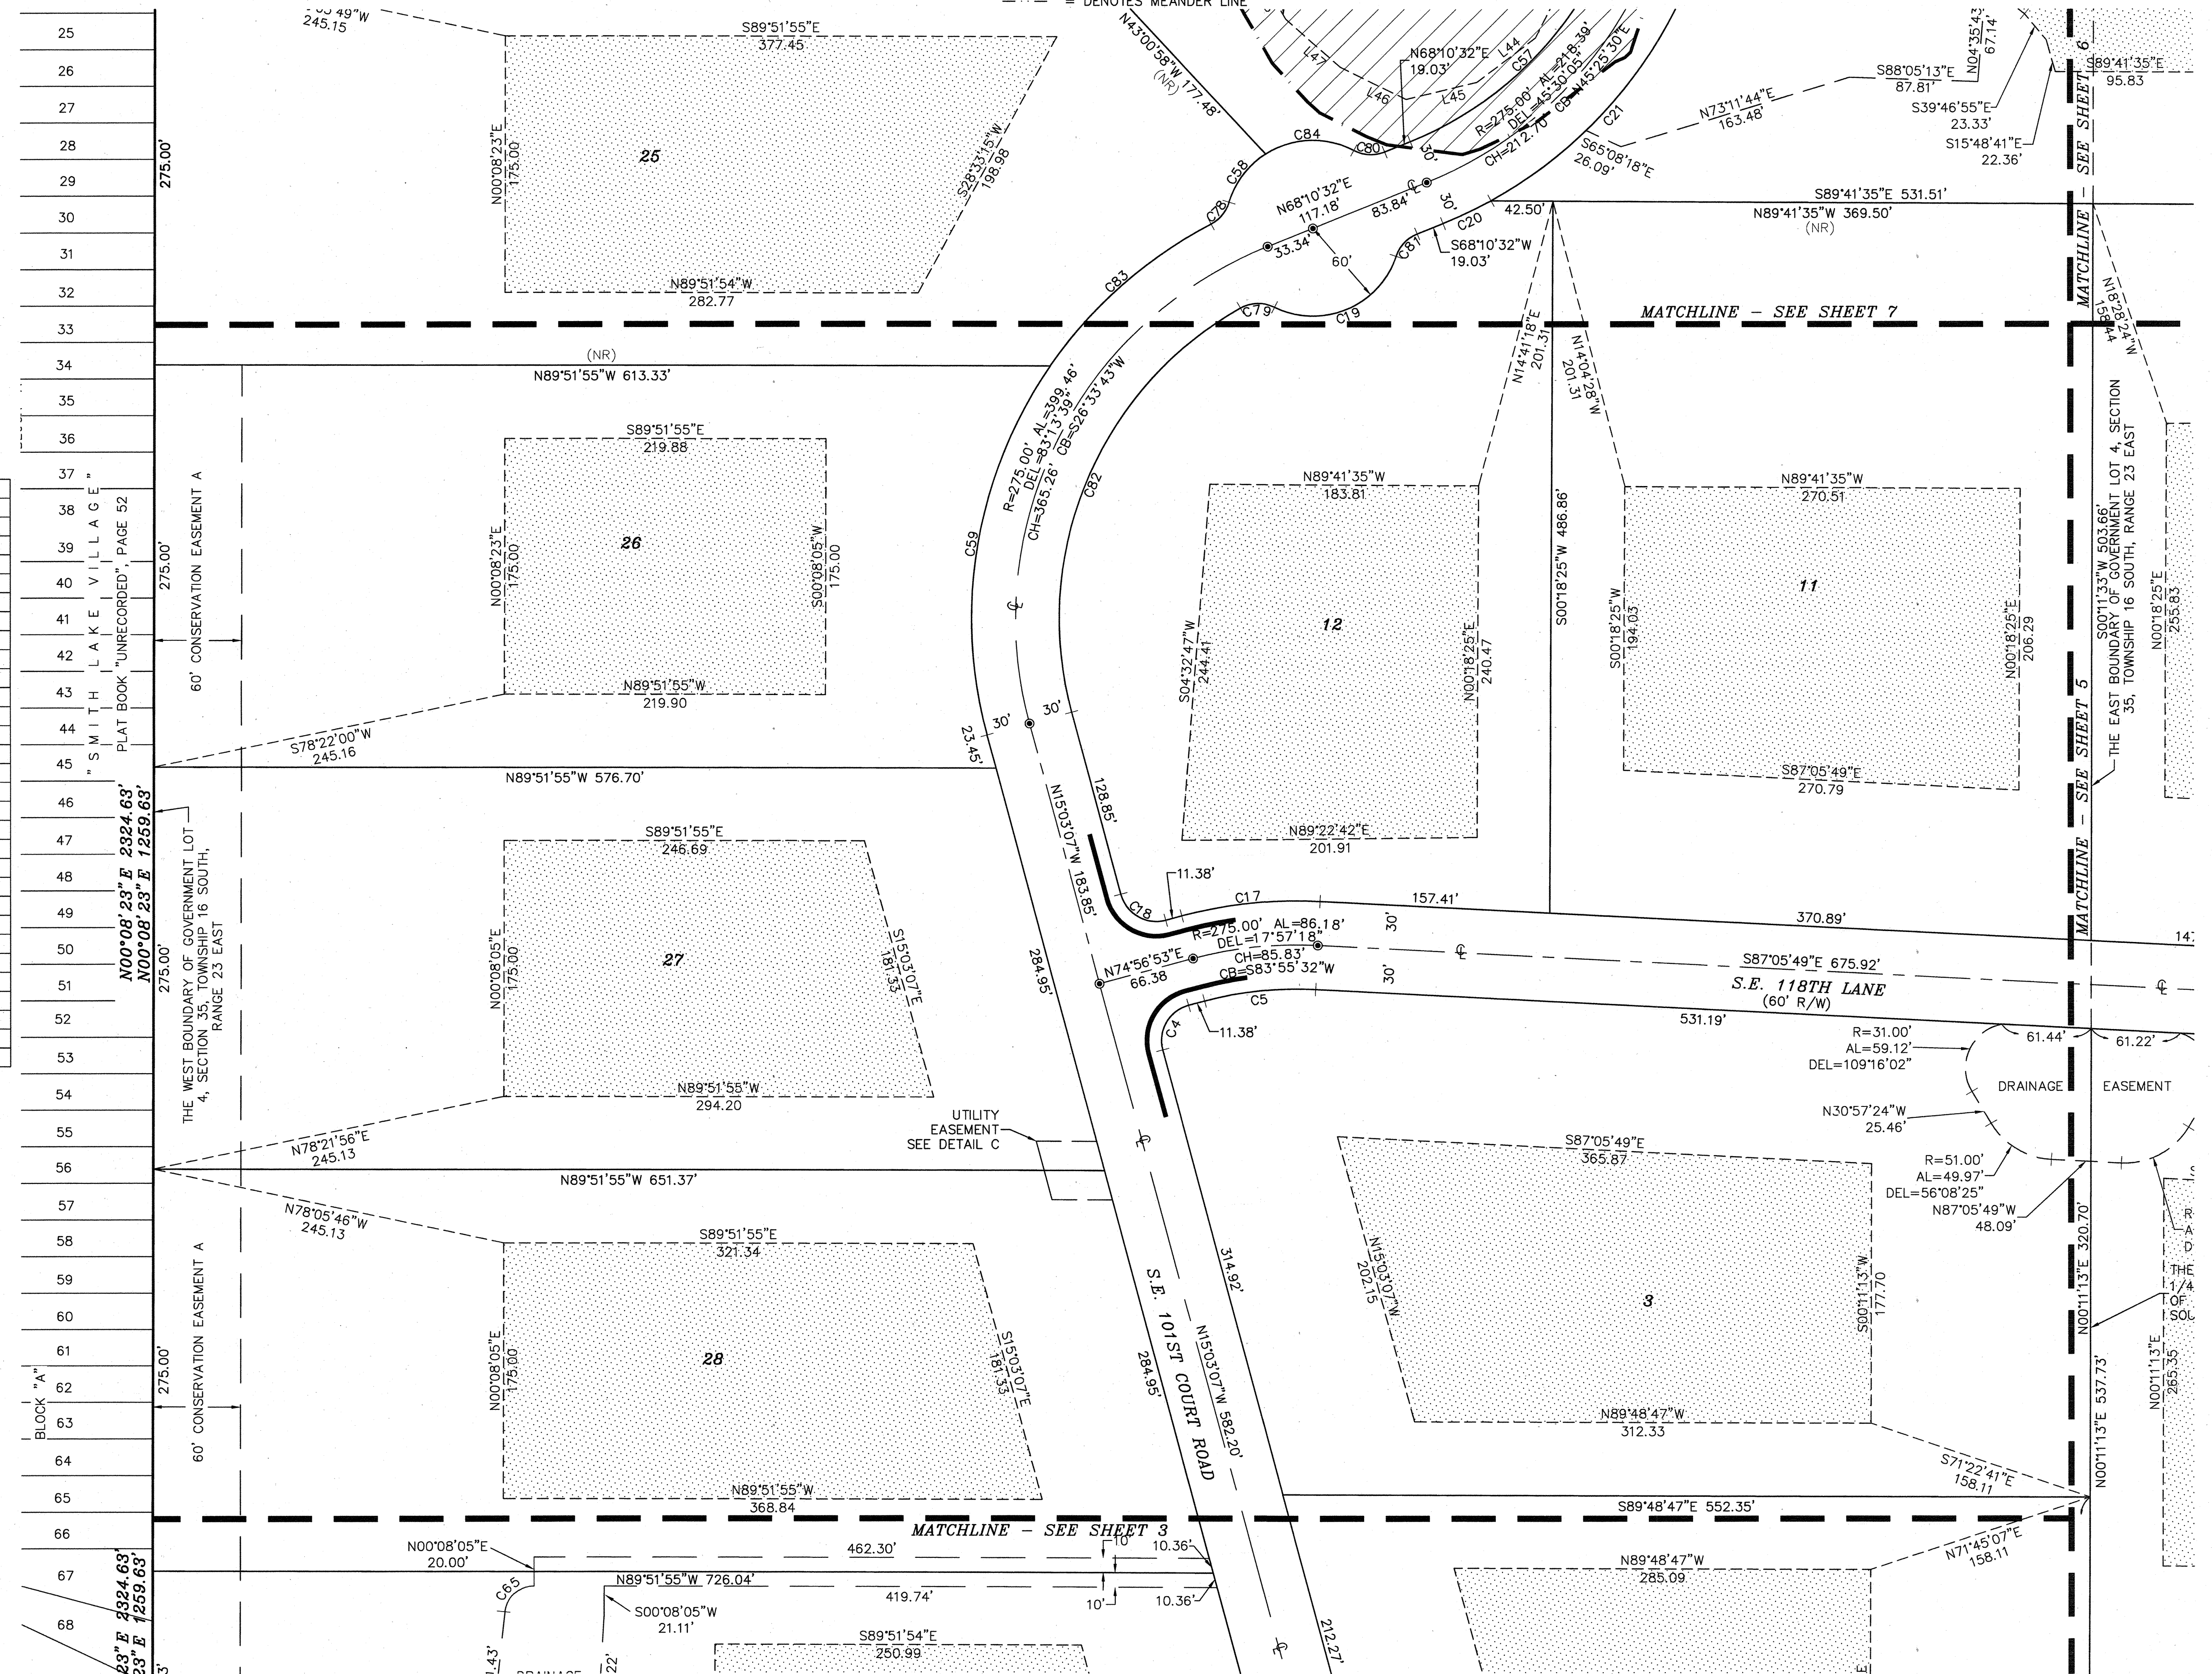

AVONLEA PHASE 1

(A HAMLET SUBDIVISION)
SECTION 35, TOWNSHIP 16 SOUTH, RANGE 23 EAST &
SECTION 2, TOWNSHIP 17 SOUTH, RANGE 23 EAST,
MARION COUNTY, FLORIDA

NOTE:
10' UTILITY EASEMENT RESERVED ALONG
AND ADJACENT TO RIGHTS-OF-WAYS

LEGEND: UNLESS OTHERWISE NOTED

PLAT BOOK 10, PAGE 199


SHEET 5 OF 9

NO.	DELTA	RADIUS	LENGTH	TANGENT	CHORD	C.B.
C6	20°02'43"	500.00'	174.93'	88.37'	174.04'	N77°04'28"W
C7	4°00'54"	560.00'	39.24'	19.63'	39.23'	S69°03'34"E
C8	18°37'34"	560.00'	182.05'	91.83'	181.25'	S80°22'48"E
C9	49°40'47"	25.00'	21.68'	11.57'	21.00'	N64°51'11"W
C10	96°23'52"	60.00'	100.95'	67.10'	89.46'	S88°12'44"E
C11	82°50'13"	60.00'	86.75'	52.93'	79.39'	N02°10'13"E
C12	100°07'29"	60.00'	104.85'	71.66'	92.01'	N89°18'38"W
C13	49°40'47"	25.00'	21.68'	11.57'	21.00'	N65°28'01"E
C14	21°07'11"	500.00'	184.30'	93.21'	183.26'	S79°07'59"E
C15	1°31'17"	500.00'	13.28'	6.64'	13.28'	S67°48'45"E
C16	20°02'43"	560.00'	195.92'	98.97'	194.92'	N77°04'28"W

STATE PLANE COORDINATES:

POINT	NORTHING	EASTING	SCALE FACTOR
Q424	1689706.2443	660315.3325	0.999941196
COED 0028	1734962.9634	639104.6136	0.999941510
A	1713346.1737	660396.5679	0.999941197
B	1713654.0010	660396.8496	0.999941197
C	1713654.5607	660246.8371	0.999941196
D	1714914.1935	660247.8597	0.999941196
E	1716105.0015	660248.8244	0.999941196
F	1716828.3502	661905.8583	0.999941216
G	1716823.9443	662909.9979	0.999941229
H	1715713.9567	662905.1314	0.999941229
I	1714746.1303	662900.8882	0.999941228
J	1713644.6759	662896.0591	0.999941228
K	1713649.6141	661572.5766	0.999941210
L	1712939.9934	661571.4147	0.999941210

- = PERMANENT REFERENCE MONUMENT
- = SET 4"x4" CONCRETE MONUMENT NO LB5091
- = PERMANENT REFERENCE MONUMENT
- = FOUND 4"x4" CONCRETE MONUMENT
- = I.D. - MOOREHEAD ENGINEERING COMPANY
- = PERMANENT CONTROL POINT
- = SET NAIL & DISK I.D. - LB5091
- R/W = RIGHT-OF-WAY
- (NR) = NON-RADIAL
- = CENTERLINE OF RIGHT OF WAY
- = BREAKLINE NOT TO SCALE
- L.B. = LANDSCAPE BUFFER
- = DRIVEWAY PROHIBITED WITHIN THIS AREA
- = DENOTES BUILDABLE AREA
- O.R. = OFFICIAL RECORDS
- P.R.C. = POINT OF REVERSE CURVATURE
- P.C. = POINT OF CURVATURE
- P.T. = POINT OF TANGENCY
- I.D. = IDENTIFICATION
- (R) = RADIAL LINE
- (TYP) = TYPICAL
- D.E. = DRAINAGE EASEMENT
- FND = FOUND
- CON = CONCRETE
- MON = MONUMENT
- U.E. = UTILITY EASEMENT
- D.R.A. = DRAINAGE RETENTION AREA
- = DENOTES MEANDER LINE

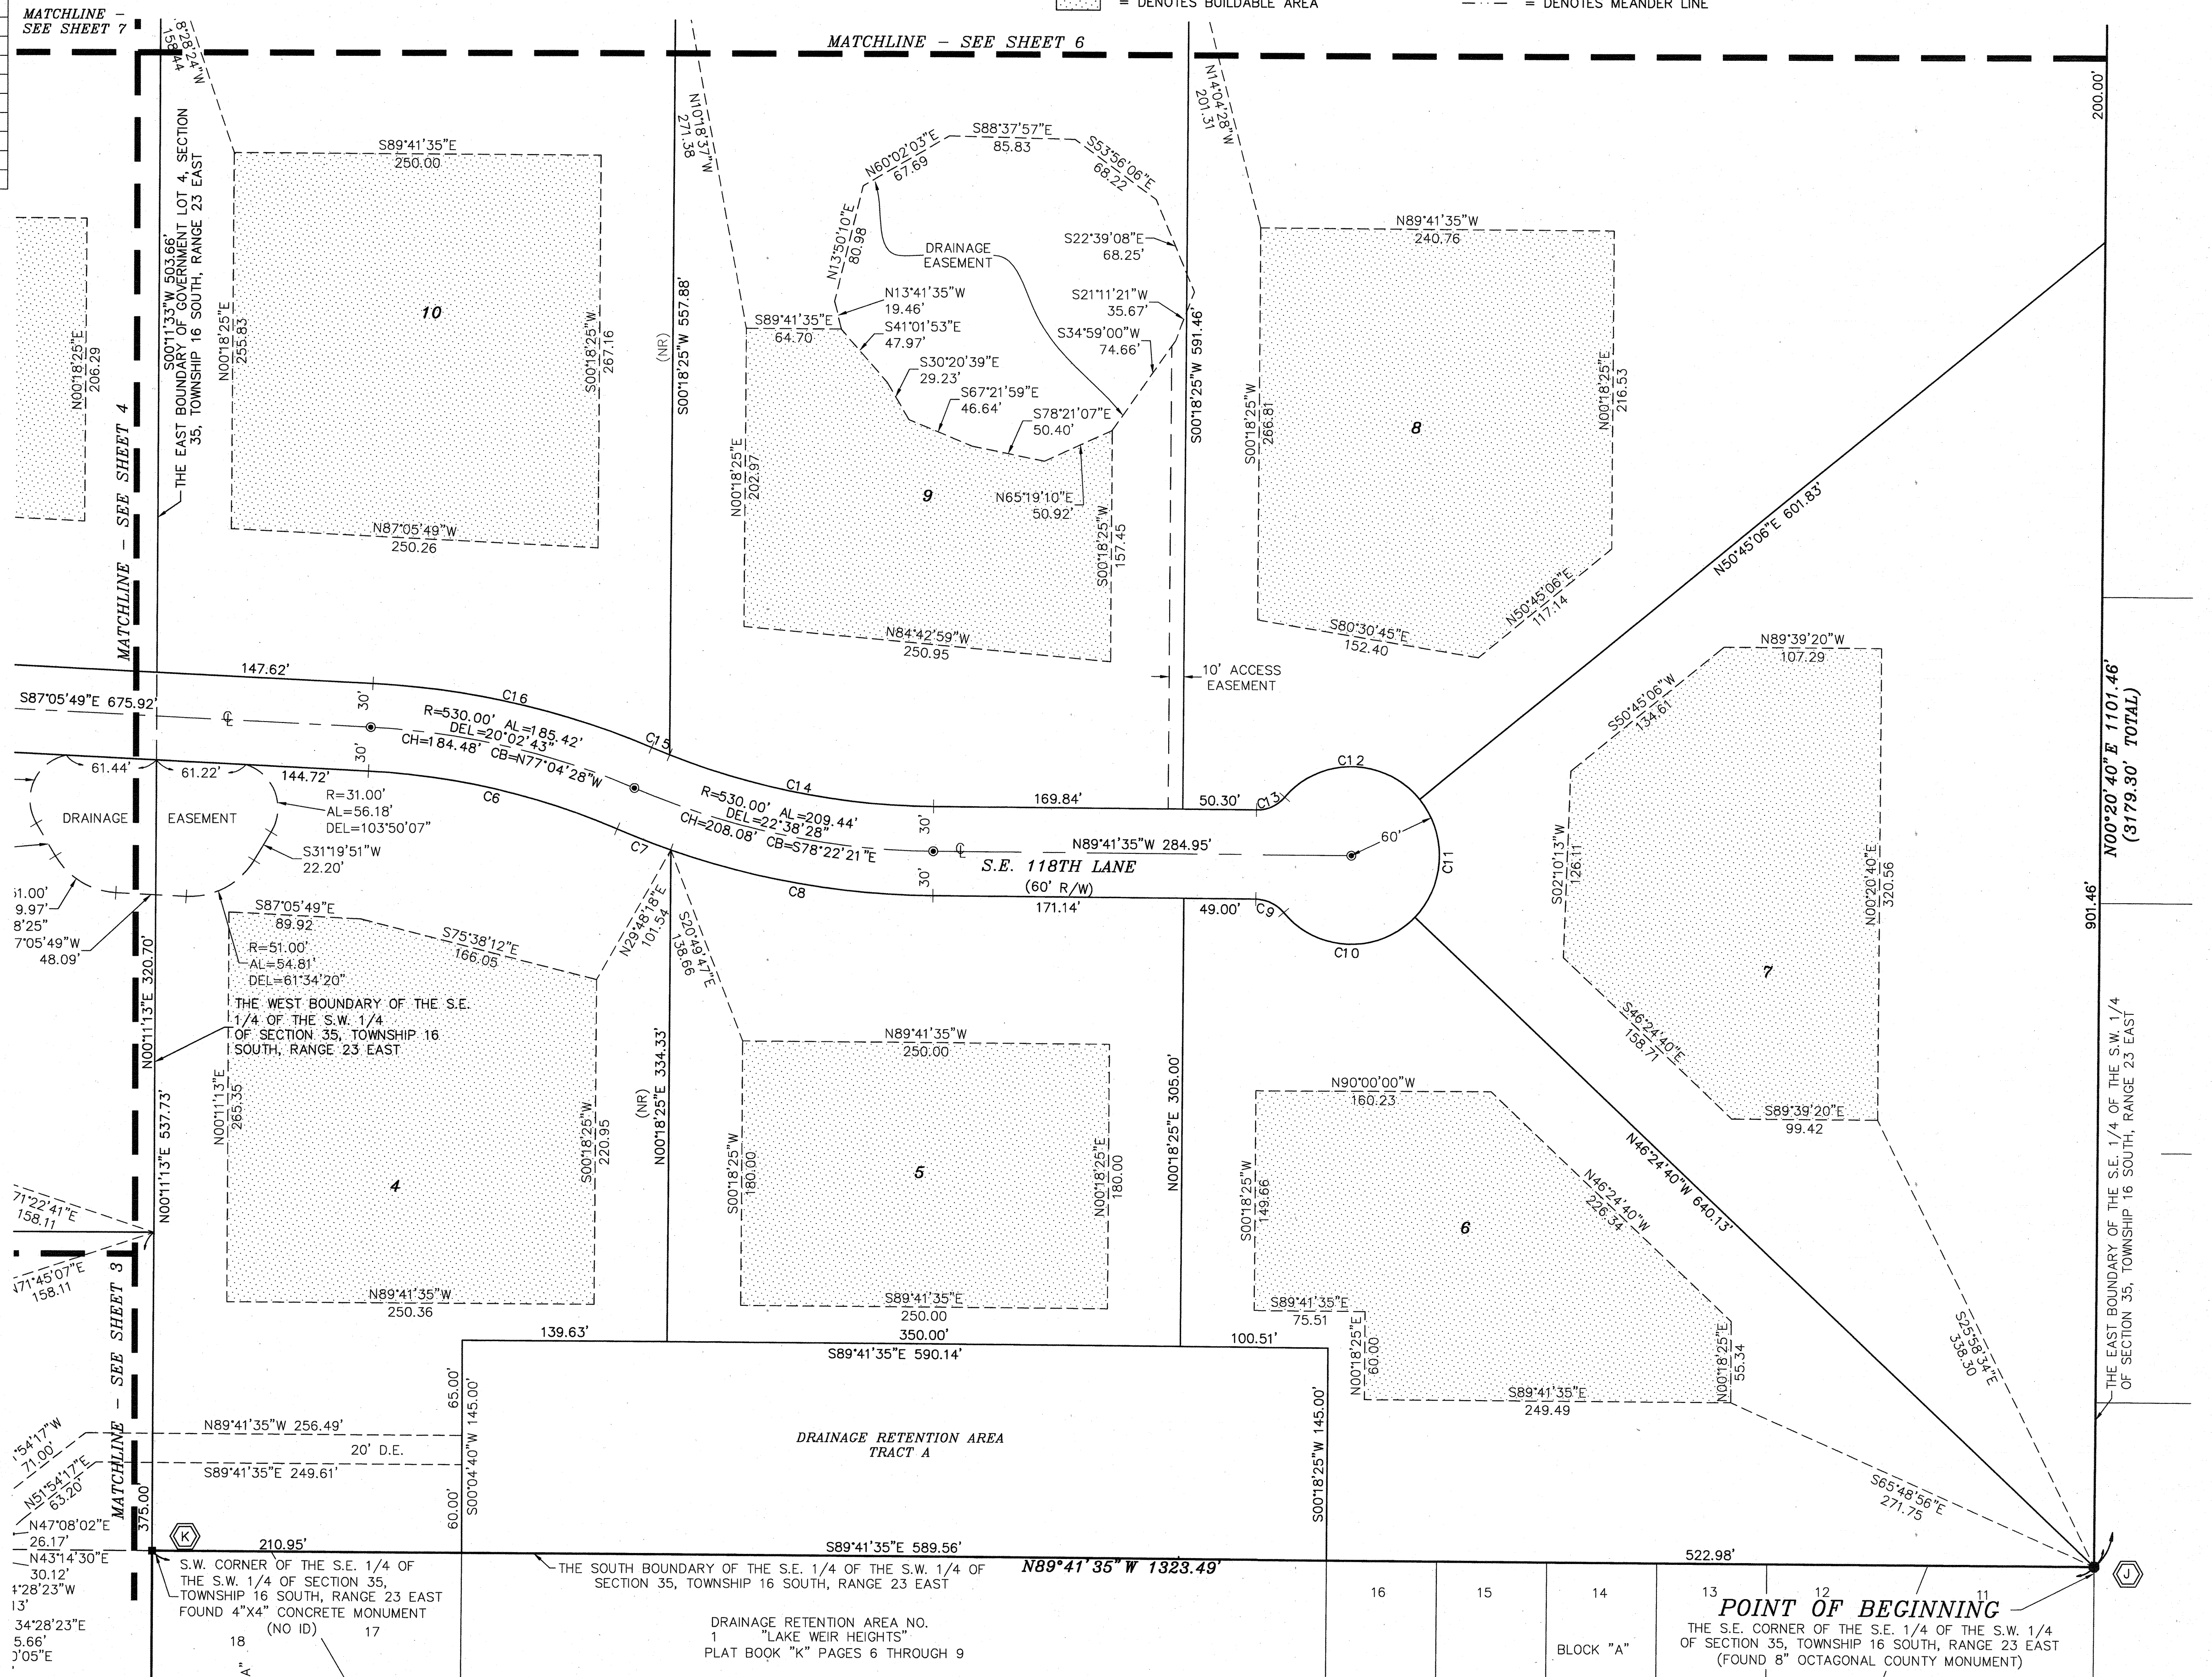

PREPARED BY: R.M. BARRINEAU & ASSOCIATES, INC. 1309 S.E. 25TH LOOP, SUITE 103 OCALA, FLORIDA 34471

R.M. BARRINEAU & ASSOCIATES, INC.
PROFESSIONAL SURVEYORS & MAPPERS
OAKHURST PROFESSIONAL PARK
1309 S.E. 25TH LOOP, SUITE 103 PHONE (352) 622-3133
OCALA, FLORIDA 34471 FAX (352) 369-3771
REGINALD M. BARRINEAU, P.S.M. - FOUNDER
CERTIFICATE OF AUTHORIZATION NO. LB 5091
KEVIN J. FLANAGAN, P.S.M. - LS 3842 CHRISTOPHER J. HOWSON, P.S.M. - LS 8553
MELVIN A. BOWEN, P.S.M. - LS 5035

AVONLEA PHASE 1

(A HAMLET SUBDIVISION)
SECTION 35, TOWNSHIP 16 SOUTH, RANGE 23 EAST &
SECTION 2, TOWNSHIP 17 SOUTH, RANGE 23 EAST,
MARION COUNTY, FLORIDA


NOTE:
10' UTILITY EASEMENT RESERVED ALONG
AND ADJACENT TO RIGHTS-OF-WAYS

CURVE TABLE


NO.	DELTA	RADIUS	LENGTH	TANGENT	CHORD	C.B.
C22	68°12'26"	340.00'	404.75'	230.23'	381.27'	S56°46'41"W
C23	15°06'36"	460.00'	121.31'	61.01'	120.96'	N83°19'36"E
C24	22°01'15"	460.00'	176.79'	89.50'	175.71'	N64°45'40"E
C25	45°44'00"	25.00'	19.95'	10.54'	19.43'	S76°37'03"W
C26	53°52'16"	60.00'	56.41'	30.49'	54.36'	N72°32'55"E
C27	53°52'16"	60.00'	56.41'	30.49'	54.36'	N18°40'39"E
C28	45°44'00"	25.00'	19.95'	10.54'	19.43'	S14°36'31"W
C29	15°46'14"	460.00'	126.61'	63.71'	126.22'	N29°35'24"E
C30	21°21'37"	460.00'	171.49'	86.75'	170.50'	N11°01'28"E
C39	36°00'42"	400.00'	251.41'	130.01'	247.29'	N18°21'01"E
C40	54°28'00"	25.00'	23.77'	12.87'	22.88'	N63°35'22"E
C42	90°25'10"	60.00'	94.69'	60.44'	85.16'	N45°36'47"E
C43	54°28'00"	25.00'	23.77'	12.87'	22.88'	N27°38'12"E
C44	36°00'42"	400.00'	251.41'	130.01'	247.29'	N72°52'33"E
C45	33°38'30"	400.00'	234.86'	120.93'	231.50'	S74°03'39"W
C46	77°05'32"	25.00'	33.64'	19.92'	31.16'	S84°12'50"E
C47	45°48'09"	245.00'	195.85'	103.50'	190.68'	S22°46'00"E
C48	49°40'47"	25.00'	21.68'	11.57'	21.00'	S24°58'29"W
C49	79°22'03"	60.00'	83.11'	49.78'	76.63'	N10°07'51"E
C66	77°45'23"	21.00'	28.50'	16.93'	26.36'	N85°18'24"E
C67	90°00'45"	21.00'	32.99'	21.00'	29.70'	N39°32'09"W
C68	17°54'05"	188.32'	58.84'	29.66'	58.60'	N14°25'16"E
C69	16°20'00"	188.32'	53.68'	27.02'	53.50'	N38°15'42"E

STATE PLANE COORDINATES:

POINT	NORTHING	EASTING	SCALE FACTOR
Q424	1689706.2443	660315.3325	0.999941196
COED 0028	1734962.9634	639104.6136	0.999941510
A	1713346.1737	660396.5679	0.999941197
B	1713654.0010	660396.8496	0.999941197
C	1713654.5607	660246.8371	0.999941196
D	1714914.1935	660247.8597	0.999941196
E	1716105.0015	660248.8244	0.999941196
F	1716828.3502	661905.8583	0.999941216
G	1716823.9443	662909.9979	0.999941229
H	1715713.9567	662905.1314	0.999941229
I	1714746.1303	662900.8882	0.999941228
J	1713644.6759	662896.0591	0.999941228
K	1713649.6141	661572.5766	0.999941210
L	1712939.9934	661571.4147	0.999941210

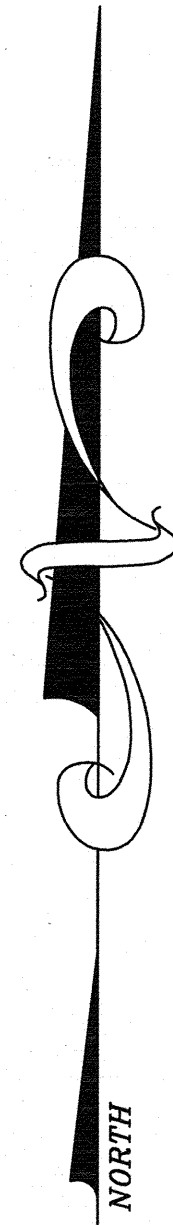

GRAPHIC SCALE

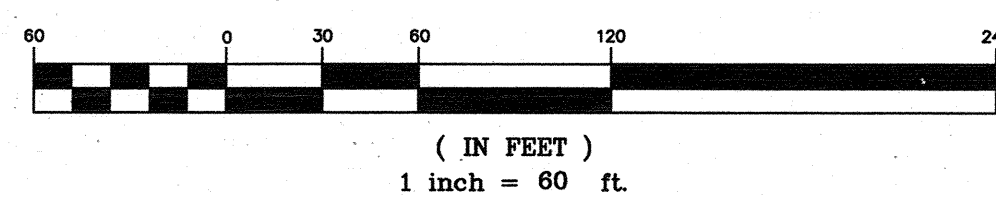


R.M. BARRINEAU & ASSOCIATES, INC.
PROFESSIONAL SURVEYORS & MAPPERS
OAKHURST PROFESSIONAL PARK
1309 S.E. 25TH LOOP, SUITE 103 PHONE (352) 622-3133
OCALA, FLORIDA 34471 FAX (352) 369-3771
REGINALD M. BARRINEAU, P.S.M. - FOUNDER
CERTIFICATE OF AUTHORIZATION NO. LB 5091
KEVIN J. FLANAGAN, P.S.M. - LS 3942 CHRISTOPHER J. HOBSON, P.S.M. - LS 6553
MELVIN A. BOWEN, P.S.M. - LS 5035

LEGEND: UNLESS OTHERWISE NOTED

- = PERMANENT REFERENCE MONUMENT
- = SET 4"x4" CONCRETE MONUMENT NO LB5091
- = PERMANENT REFERENCE MONUMENT FOUND 4"x4" CONCRETE MONUMENT
- = I.D. - MOORHEAD ENGINEERING COMPANY
- = PERMANENT CONTROL POINT
- = SET NAIL & DISK I.D. - LB5091
- R/W = RIGHT-OF-WAY
- (NR) = NON-RADIAL
- = CENTERLINE OF RIGHT OF WAY
- - - = BREAKLINE NOT TO SCALE
- ▨ = DENOTES BUILDABLE AREA
- L.B. = LANDSCAPE BUFFER
- O.R. = OFFICIAL RECORDS
- P.R.C. = POINT OF REVERSE CURVATURE
- P.C. = POINT OF CURVATURE
- P.T. = POINT OF TANGENCY
- I.D. = IDENTIFICATION
- (R) = RADIAL LINE
- (TYP) = TYPICAL
- D.E. = DRAINAGE EASEMENT
- U.E. = UTILITY EASEMENT
- D.R.A. = DRAINAGE RETENTION AREA
- = DRIVEWAY PROHIBITED WITHIN THIS AREA
- - - = DENOTES MEANDER LINE

PLAT BOOK 10, PAGE 200
SHEET 6 OF 9

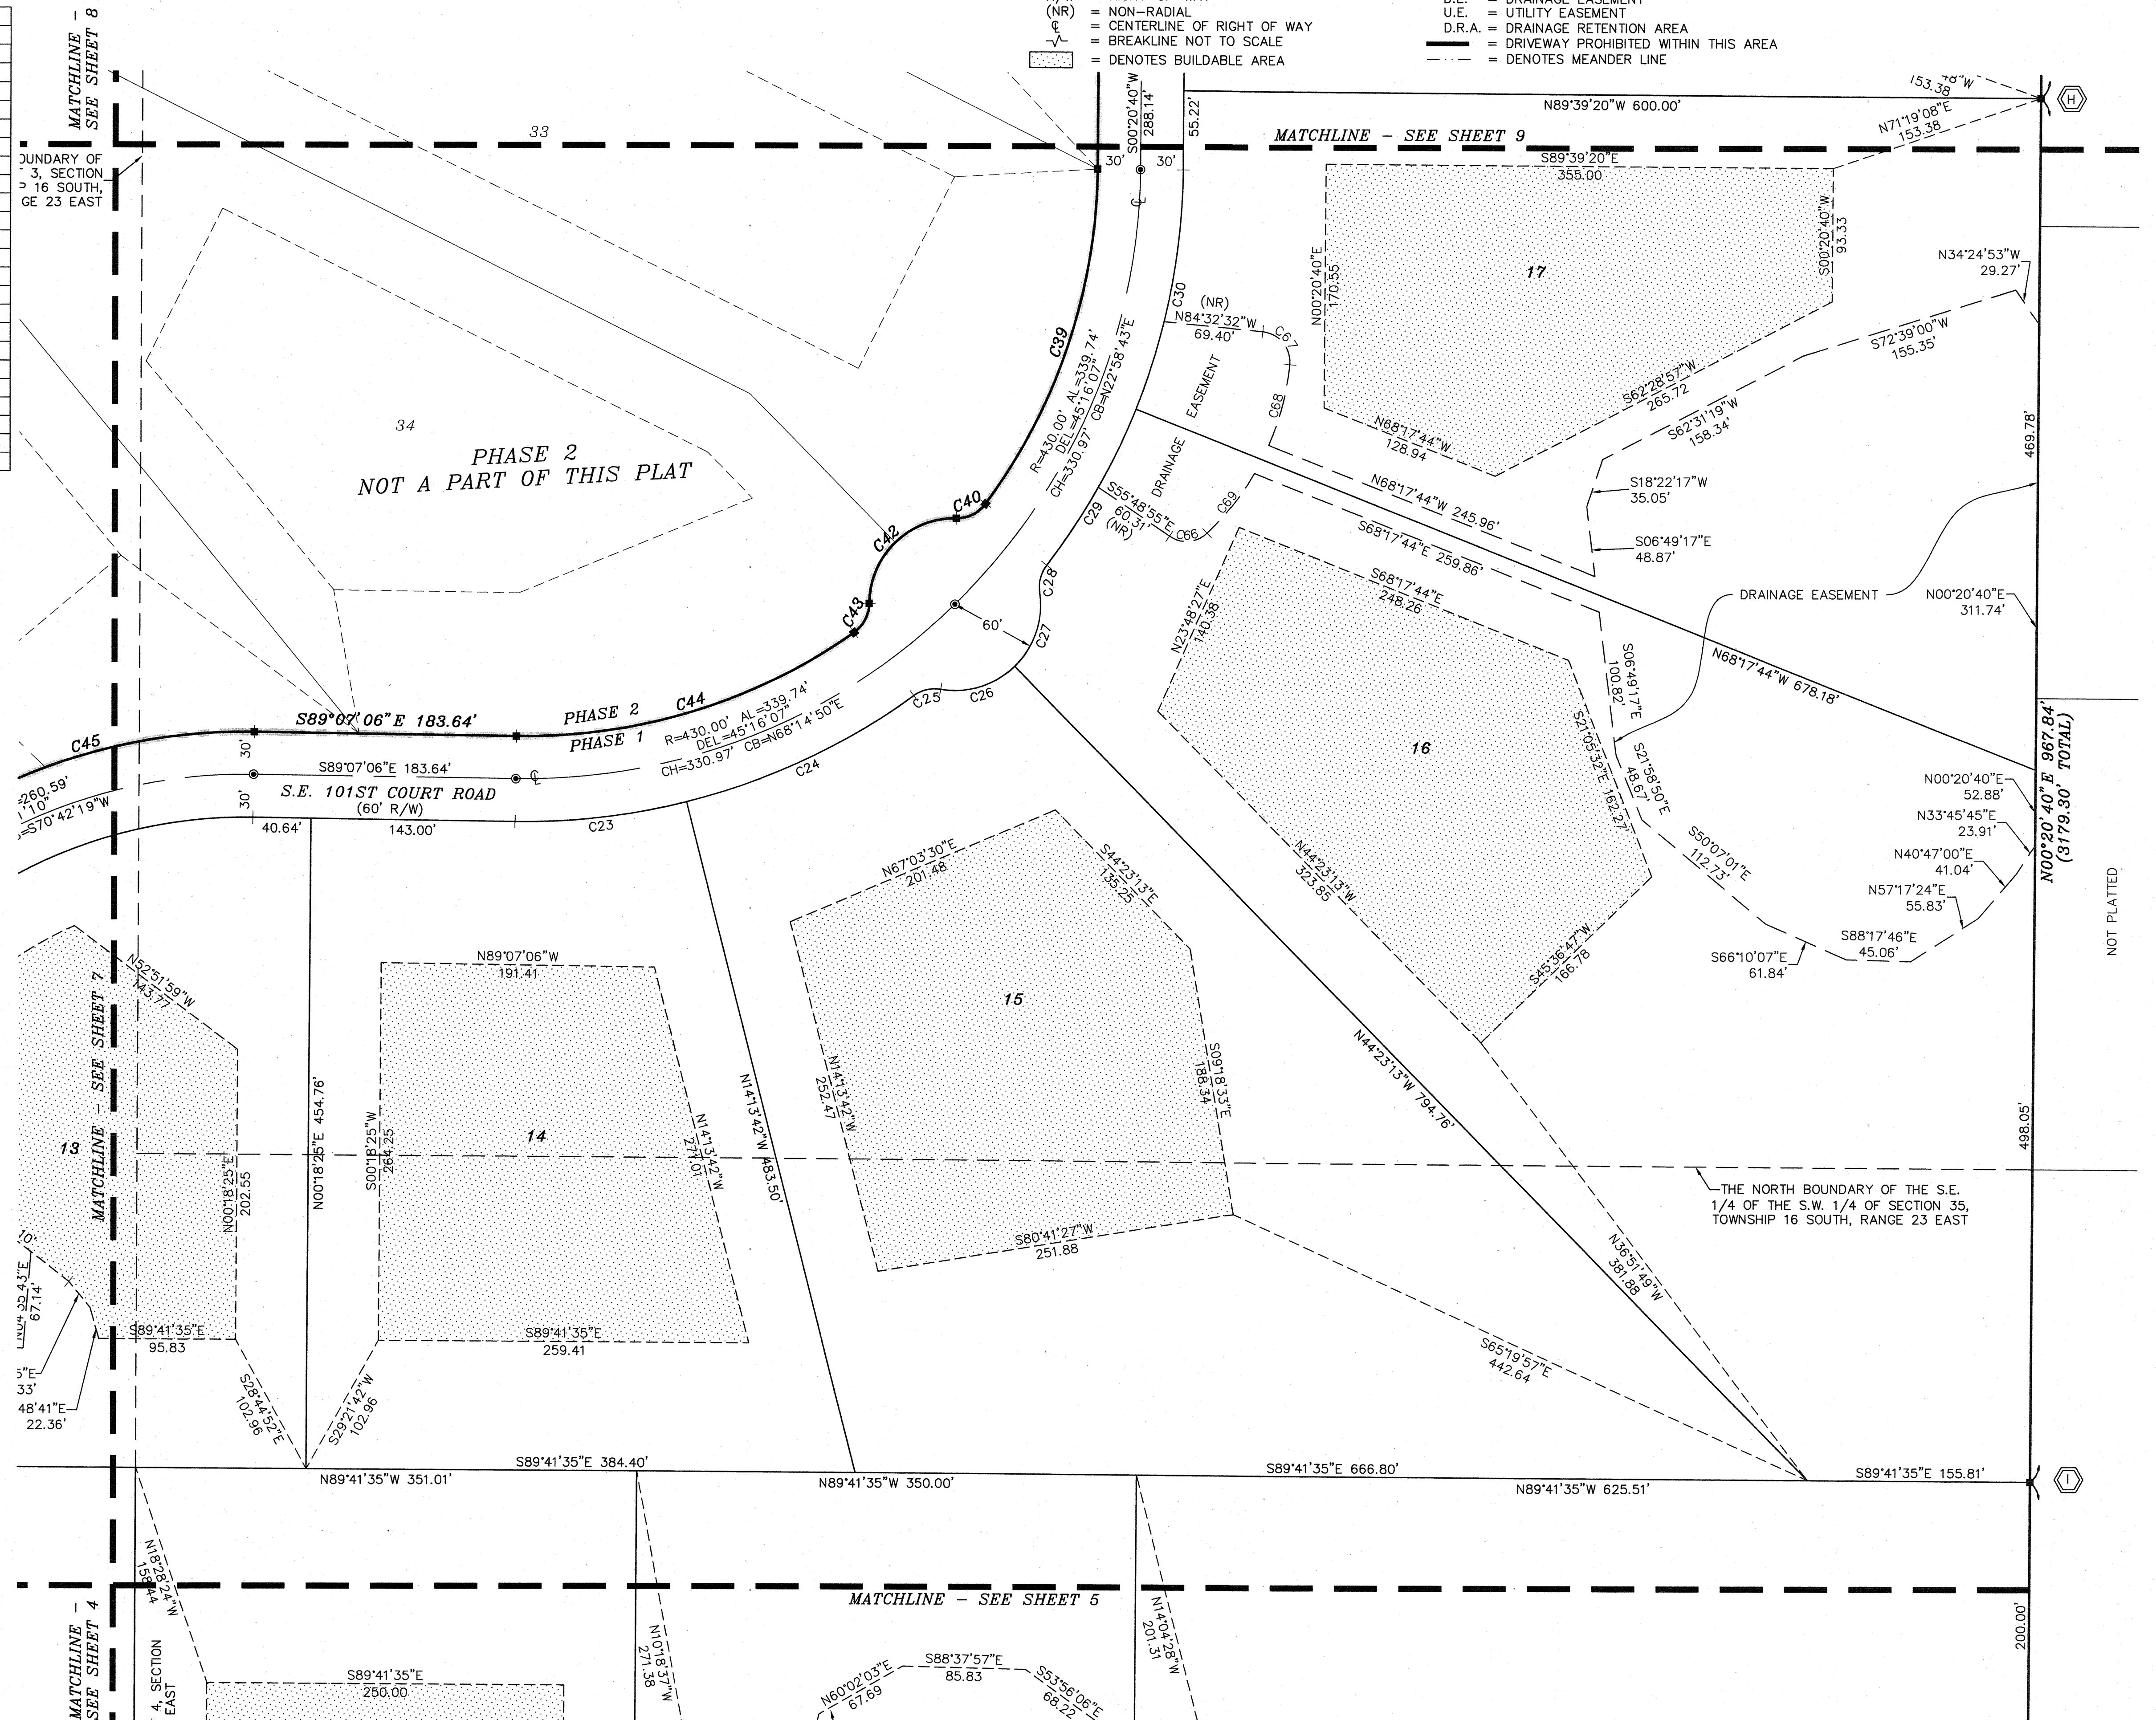

AVONLEA PHASE 1

(A HAMLET SUBDIVISION)
SECTION 35, TOWNSHIP 16 SOUTH, RANGE 23 EAST &
SECTION 2, TOWNSHIP 17 SOUTH, RANGE 23 EAST,
MARION COUNTY, FLORIDA

LEGEND: UNLESS OTHERWISE NOTED

- = PERMANENT REFERENCE MONUMENT
- = SET 4"x4" CONCRETE MONUMENT NO LB5091
- = PERMANENT REFERENCE MONUMENT FOUND 4"x4" CONCRETE MONUMENT I.D. - MOOREHEAD ENGINEERING COMPANY
- = PERMANENT CONTROL POINT
- = SET NAIL & DISK I.D. - LB5091
- R/W = RIGHT-OF-WAY
- (NR) = NON-RADIAL
- ⊥ = CENTERLINE OF RIGHT OF WAY
- = BREAKLINE NOT TO SCALE
- L.B. = LANDSCAPE BUFFER
- O.R. = OFFICIAL RECORDS
- P.R.C. = POINT OF REVERSE CURVATURE
- P.C. = POINT OF CURVATURE
- P.T. = POINT OF TANGENCY
- I.D. = IDENTIFICATION
- (R) = RADIAL LINE
- (TYP) = TYPICAL
- D.E. = DRAINAGE EASEMENT
- U.E. = UTILITY EASEMENT
- D.R.A. = DRAINAGE RETENTION AREA
- = DRIVEWAY PROHIBITED WITHIN THIS AREA
- = DENOTES BUILDABLE AREA
- = DENOTES MEANDER LINE

PLAT BOOK 10, PAGE 201

SHEET 7 OF 9

GRAPHIC SCALE



(IN FEET)
1 inch = 60 ft.

NOTE:
10' UTILITY EASEMENT RESERVED ALONG
AND ADJACENT TO RIGHTS-OF-WAYS

CURVE TABLE						
NO.	DELTA	RADIUS	LENGTH	TANGENT	CHORD	C.B.
C19	97°33'16"	60.00'	102.16'	68.48'	90.26'	N67°16'23"E
C20	6°48'23"	305.00'	36.23'	18.14'	36.21'	N64°46'21"E
C21	38°41'42"	305.00'	205.98'	107.09'	202.09'	N42°01'18"E
C22	68°12'26"	340.00'	404.75'	230.23'	381.27'	S56°46'41"W
C45	33°38'30"	400.00'	234.86'	120.93'	231.50'	S74°03'39"W
C46	77°05'32"	25.00'	33.64'	19.92'	31.16'	S84°12'50"E
C55	87°58'08"	25.00'	38.38'	24.13'	34.72'	N01°41'00"W
C56	19°37'37"	400.00'	137.02'	69.19'	136.35'	S32°29'16"W
C57	45°30'05"	245.00'	194.57'	102.74'	189.49'	N45°25'30"E
C58	40°19'57"	60.00'	42.24'	22.04'	41.37'	S37°13'51"W
C70	126°33'05"	16.00'	35.34'	31.78'	28.58'	S83°04'36"W
C71	108°15'50"	31.00'	58.58'	42.88'	50.24'	N34°19'52"W
C72	54°48'55"	50.00'	47.84'	25.93'	46.03'	S61°03'19"E
C73	115°22'15"	26.00'	52.35'	41.10'	43.95'	S13°21'11"E
C74	32°42'35"	50.00'	28.54'	14.67'	28.16'	N45°21'24"W
C75	102°09'08"	25.00'	44.57'	30.96'	38.90'	S80°04'40"E
C78	45°24'13"	25.00'	19.81'	10.46'	19.30'	N39°45'59"E
C79	55°38'01"	25.00'	24.27'	13.19'	23.33'	S88°14'01"W
C80	49°40'47"	25.00'	21.68'	11.57'	21.00'	S86°59'04"E
C81	49°40'47"	25.00'	21.68'	11.57'	21.00'	S43°20'09"W
C82	75°28'08"	245.00'	322.71'	189.59'	299.88'	S22°40'57"W
C83	27°53'53"	305.00'	148.51'	75.76'	147.05'	S48°31'08"W
C84	60°27'30"	60.00'	63.31'	34.96'	60.42'	S87°37'35"W

LINE TABLE				LINE TABLE			
LINE	LENGTH	BEARING		LINE	LENGTH	BEARING	
L1	50.47'	S58°25'59"W	L47	50.00'	N48°39'56"W		
L2	57.68'	S33°38'52"E	L48	50.00'	N28°45'10"W		
L3	62.42'	N19°48'03"E	L49	16.86'	N09°58'53"E		
L4	41.34'	S19°48'03"W	L50	132.89'	N17°31'47"E		
L5	25.25'	S88°27'47"E	L51	191.50'	S21°10'40"W		
L6	58.72'	N44°19'56"E	L52	164.56'	S28°20'40"W		
L7	63.52'	N29°00'06"W	L53	118.09'	S38°15'06"W		
L8	31.42'	S48°50'47"W	L54	77.93'	S52°55'10"W		
L9	6.68'	N71°02'19"W	L55	79.99'	S67°00'42"W		
L10	59.94'	N61°42'41"W	L56	72.01'	S82°18'03"W		
L11	50.24'	N26°11'15"E	L57	51.00'	N82°50'26"W		
L12	50.00'	N05°54'55"E	L58	82.19'	S24°12'29"E		
L13	50.00'	N06°21'19"W	L59	109.30'	S07°13'11"E		
L14	50.00'	N25°39'19"W	L60	107.03'	S10°19'48"W		
L15	50.00'	N43°44'51"W	L61	103.84'	S28°13'07"W		
L16	50.00'	N62°28'20"W	L62	97.50'	S46°38'19"W		
L17	50.00'	N75°02'44"W	L63	87.29'	S66°17'24"W		
L18	50.00'	N82°48'56"W	L64	80.23'	S89°46'35"W		
L19	50.00'	S86°45'53"W	L65	84.01'	N66°13'50"W		
L20	50.00'	S75°49'01"W	L66	88.29'	N45°20'49"W		
L21	50.00'	S56°14'24"W	L67	95.49'	N24°17'29"W		
L22	50.00'	S39°54'32"W	L68	90.56'	N00°12'38"W		
L23	50.00'	S23°03'03"W	L69	111.93'	N22°37'54"E		
L24	50.00'	S02°05'16"W	L70	102.20'	N38°58'10"E		
L25	50.00'	S18°34'20"E	L71	110.08'	N53°48'11"E		
L26	50.00'	S36°53'46"E	L72	85.24'	N74°36'32"E		
L27	50.00'	S51°00'23"E	L73	207.51'	N60°52'50"W		
L28	50.00'	S59°26'05"E	L74	95.46'	N44°09'17"W		
L29	50.00'	S71°21'00"E	L75	143.10'	N26°06'34"W		
L30	50.00'	S82°13'55"E	L76	58.79'	N52°42'21"W		
L31	50.00'	N82°33'29"E	L77	80.47'	N85°37'34"W		
L32	50.00'	N62°01'09"E	L78	149.97'	S84°52'52"W		
L33	50.00'	N52°22'46"E	L79	29.04'	S38°23'45"W		
L34	19.84'	N37°17'10"E	L80	64.50'	S21°35'23"W		
L35	50.00'	N08°50'39"E	L81	79.46'	S35°53'47"W		
L36	50.00'	N28°17'17"E	L82	56.61'	S44°51'56"W		
L37	50.00'	N54°34'52"E	L83	80.06'	S16°16'41"W		
L38	50.00'	N89°56'35"E	L84	50.52'	S14°08'23"W		
L39	50.00'	S68°01'00"E	L85	72.05'	S25°58'37"W		
L40	50.00'	S42°53'47"E	L86	78.78'	S41°14'03"W		
L41	50.00'	S21°42'22"E	L87	101.32'	S52°43'30"W		
L42	50.00'	S07°13'26"W	L88	71.58'	S61°22'07"W		
L43	50.00'	S26°54'23"W	L89	49.34'	S11°17'52"E		
L44	50.00'	S52°55'32"W	L97	24.67'	N73°20'32"W		
L45	50.00'	S76°26'40"W	L98	21.75'	N73°20'32"W		
L46	50.00'	N63°58'55"W	L99	115.67'	N42°54'57"W		
			L100	120.00'	N42°54'57"W		

R.M. BARRINEAU & ASSOCIATES, INC.

PROFESSIONAL SURVEYORS & MAPPERS

OAKHURST PROFESSIONAL PARK

1309 S.E. 25TH LOOP, SUITE 103 Ocala, FLORIDA 34471

PHONE (352) 622-3133 FAX (352) 369-3771

REGINALD M. BARRINEAU, P.S.M. - FOUNDER

CERTIFICATE OF AUTHORIZATION NO. LB 5091

KEVIN J. FLANAGAN, P.S.M. - LS 3942 CHRISTOPHER J. HOWSON, P.S.M. - LS 6553


MELVIN A. BOWEN, P.S.M. - LS 5035

AVONLEA PHASE 1

(A HAMLET SUBDIVISION)
SECTION 35, TOWNSHIP 16 SOUTH, RANGE 23 EAST &
SECTION 2, TOWNSHIP 17 SOUTH, RANGE 23 EAST,
MARION COUNTY, FLORIDA

LINE TABLE		
LINE	LENGTH	BEARING
L1	50.47'	S58°25'59"W
L2	57.68'	S33°38'52"E
L3	62.42'	N19°48'03"E
L4	41.34'	S19°48'03"W
L5	25.25'	S88°27'47"E
L6	58.72'	N44°19'56"E
L7	63.52'	N29°00'06"W
L8	31.42'	S48°50'47"W
L9	6.68'	N71°02'19"W
L10	59.94'	N61°42'41"W
L11	50.24'	N26°11'15"E
L12	50.00'	N05°54'55"E
L13	50.00'	N06°21'19"W
L14	50.00'	N25°39'19"W
L15	50.00'	N43°44'51"W
L16	50.00'	N62°28'20"W
L17	50.00'	N75°02'44"W
L18	50.00'	N82°48'56"W
L19	50.00'	S86°45'53"W
L20	50.00'	S75°49'01"W
L21	50.00'	S56°14'24"W
L22	50.00'	S39°54'32"W
L23	50.00'	S23°03'03"W
L24	50.00'	S02°05'16"W
L25	50.00'	S18°34'20"E
L26	50.00'	S36°53'46"E
L27	50.00'	S51°00'23"E
L28	50.00'	S59°26'05"E
L29	50.00'	S71°21'00"E
L30	50.00'	S82°13'55"E
L31	50.00'	N82°33'29"E
L32	50.00'	N62°01'09"E
L33	50.00'	N52°22'46"E
L34	19.84'	N37°17'10"E
L35	50.00'	N08°50'39"E
L36	50.00'	N28°17'17"E
L37	50.00'	N54°34'52"E
L38	50.00'	N89°56'35"E
L39	50.00'	S68°01'00"E
L40	50.00'	S42°53'47"E
L41	50.00'	S21°42'22"E
L42	50.00'	S07°13'26"W
L43	50.00'	S26°54'23"W
L44	50.00'	S52°55'32"W
L45	50.00'	S76°26'40"W
L46	50.00'	N63°58'55"W
L47	50.00'	N48°39'56"W
L48	50.00'	N28°45'10"W
L49	16.86'	N09°58'53"E
L50	132.89'	N17°31'47"E
L51	191.50'	S21°10'40"W
L52	164.56'	S28°20'40"W
L53	118.09'	S38°15'06"W
L54	77.93'	S52°55'10"W
L55	79.99'	S67°00'42"W
L56	72.01'	S82°18'03"W
L57	51.00'	N82°50'26"W
L58	82.19'	S24°12'29"E
L59	109.30'	S07°13'11"E
L60	107.03'	S10°19'48"W
L61	103.84'	S28°13'07"W
L62	97.50'	S46°38'19"W
L63	87.29'	S66°17'24"W
L64	80.23'	S89°46'35"W
L65	84.01'	N66°13'50"W
L66	88.29'	N45°20'49"W
L67	95.49'	N24°17'29"W
L68	90.56'	N00°12'38"W
L69	111.93'	N22°37'54"E
L70	102.20'	N38°58'10"E
L71	110.08'	N53°48'11"E
L72	85.24'	N74°36'32"E
L73	207.51'	N60°52'50"W
L74	95.46'	N44°09'17"W
L75	143.10'	N26°06'34"W
L76	58.79'	N52°42'21"W
L77	80.47'	N85°37'34"W
L78	149.97'	S84°52'52"W
L79	29.04'	S38°23'45"W
L80	64.50'	S21°35'23"W
L81	79.46'	S35°53'47"W
L82	56.61'	S44°51'56"W
L83	80.06'	S16°16'41"W
L84	50.52'	S14°08'23"W
L85	72.05'	S25°58'37"W
L86	78.78'	S41°14'03"W
L87	101.32'	S52°43'30"W
L88	71.58'	S61°22'07"W
L89	49.34'	S11°17'52"E
L90	24.67'	N73°20'32"W
L91	21.75'	N73°20'32"W
L92	115.67'	N42°54'57"W
L93	120.00'	N42°54'57"W

NOTE:
10' UTILITY EASEMENT RESERVED ALONG
AND ADJACENT TO RIGHTS-OF-WAYS

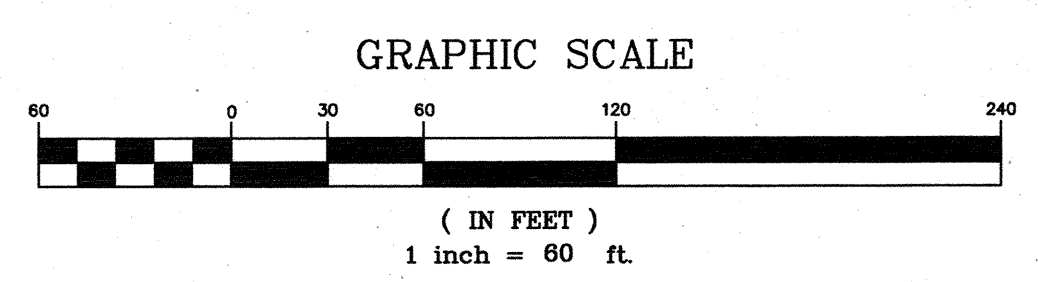


STATE PLANE COORDINATES:

POINT	NORTHING	EASTING	SCALE FACTOR
Q424	1689706.2443	660315.3325	0.999941196
COED 0028	1734962.9634	639104.6136	0.999941510
(A)	1713346.1737	660396.5679	0.999941197
(B)	1713654.0010	660396.8496	0.999941197
(C)	1713654.5607	660246.8371	0.999941196
(D)	1714914.1935	660247.8597	0.999941196
(E)	1716105.0015	660248.8244	0.999941196
(F)	1716828.3502	661905.8583	0.999941216
(G)	1716823.9443	662909.9979	0.999941229
(H)	1715713.9567	662905.1314	0.999941229
(I)	1714746.1303	662900.8882	0.999941228
(J)	1713644.6759	662896.0591	0.999941228
(K)	1713649.6141	661572.5766	0.999941210
(L)	1712939.9934	661571.4147	0.999941210

- LEGEND:** UNLESS OTHERWISE NOTED
- = PERMANENT REFERENCE MONUMENT SET 4"x4" CONCRETE MONUMENT NO LB5091
 - = PERMANENT REFERENCE MONUMENT FOUND 4"x4" CONCRETE MONUMENT I.D. - MOOREHEAD ENGINEERING COMPANY
 - = PERMANENT CONTROL POINT SET NAIL & DISK I.D. - LB5091
 - = RIGHT-OF-WAY
 - (NR) = NON-RADIAL
 - = CENTERLINE OF RIGHT OF WAY
 - = BREAKLINE NOT TO SCALE
| O.R. | = OFFICIAL RECORDS |
| P.R.C. | = POINT OF REVERSE CURVATURE |
| P.C. | = POINT OF CURVATURE |
| P.T. | = POINT OF TANGENCY |
| I.D. | = IDENTIFICATION |
| (TYP) | = TYPICAL |
| D.E. | = DRAINAGE EASEMENT |
| U.E. | = UTILITY EASEMENT |
| D.R.A. | = DRAINAGE RETENTION AREA |
| — | = DRIVEWAY PROHIBITED WITHIN THIS AREA |
| L.B. | = LANDSCAPE BUFFER |
| — | = DENOTES BUILDABLE AREA |
| — | = DENOTES MEANDER LINE |

CURVE TABLE						
NO.	DELTA	RADIUS	LENGTH	TANGENT	CHORD	C.B.
C47	45°48'09"	245.00'	195.85'	103.50'	190.68'	S22°46'00"E
C48	49°40'47"	25.00'	21.68'	11.57'	21.00'	S24°58'29"W
C49	79°22'03"	60.00'	83.11'	49.78'	76.63'	N10°07'51"E
C50	56°26'34"	60.00'	59.11'	32.20'	56.75'	N57°46'28"W
C51	93°52'10"	60.00'	98.30'	64.20'	87.67'	S47°04'10"W
C52	49°40'47"	60.00'	52.02'	27.77'	50.41'	S24°42'19"E
C53	49°40'47"	25.00'	21.68'	11.57'	21.00'	N24°42'19"W
C54	44°47'38"	305.00'	238.45'	125.69'	232.42'	S23°16'15"E
C70	126°33'05"	16.00'	35.34'	31.78'	28.58'	S83°04'36"W
C71	108°15'50"	31.00'	58.58'	42.88'	50.24'	N34°19'52"W
C72	54°48'55"	50.00'	47.84'	25.93'	46.03'	S61°03'19"E
C76	1°00'31"	305.00'	5.37'	2.68'	5.37'	S00°22'10"E

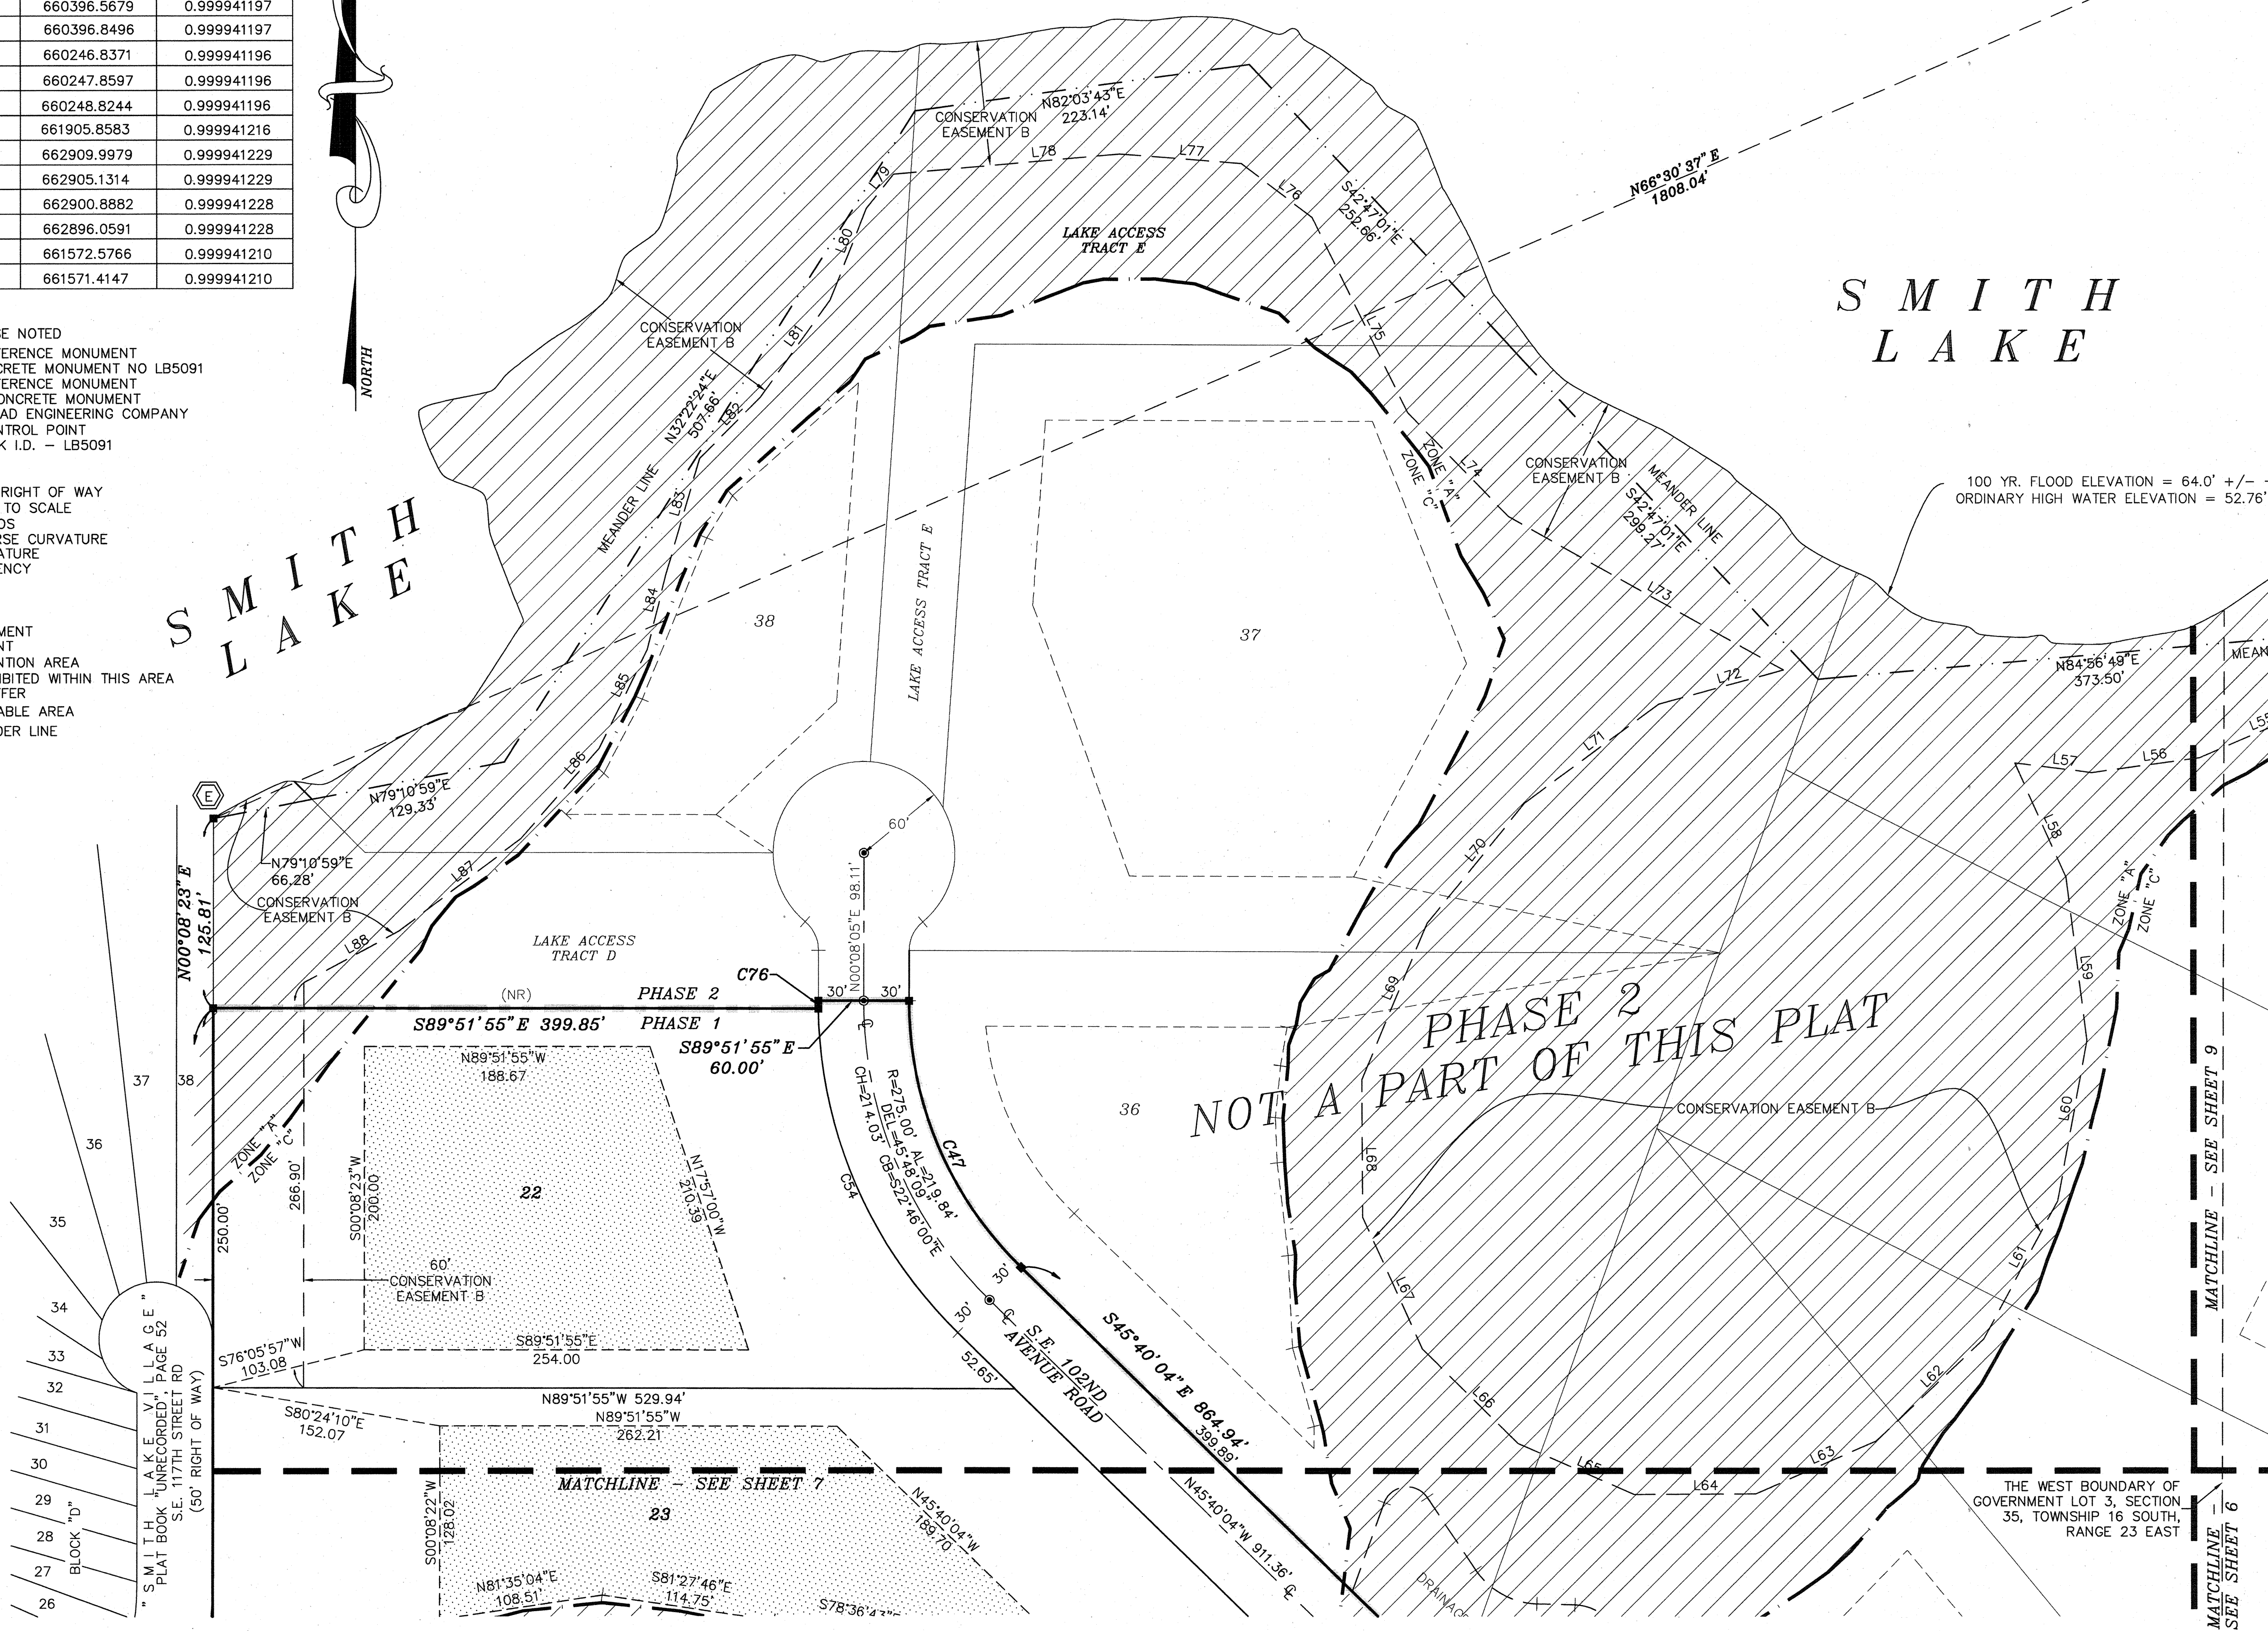

SMITH
LAKE

100 YR. FLOOD ELEVATION = 64.0' +/-
ORDINARY HIGH WATER ELEVATION = 52.76'

PHASE 2
NOT A PART OF THIS PLAT

R.M. BARRINEAU & ASSOCIATES, INC.
PROFESSIONAL SURVEYORS & MAPPERS
OAKHURST PROFESSIONAL PARK
1309 S.E. 25TH LOOP, SUITE 103 Ocala, Florida 34471
PHONE (352) 622-3133 FAX (352) 369-3771
REGINALD M. BARRINEAU, P.S.M. - FOUNDER
CERTIFICATE OF AUTHORIZATION NO. LB 5091
KEVIN J. FLANAGAN, P.S.M. - LS 3942 CHRISTOPHER J. HOWSON, P.S.M. - LS 6553
MELVIN A. BOWEN, P.S.M. - LS 5035

PREPARED BY: R.M. BARRINEAU & ASSOCIATES, INC. 1309 S.E. 25TH LOOP, SUITE 103 OCALA, FLORIDA 34471

AVONLEA PHASE 1

(A HAMLET SUBDIVISION)
SECTION 35, TOWNSHIP 16 SOUTH, RANGE 23 EAST &
SECTION 2, TOWNSHIP 17 SOUTH, RANGE 23 EAST,
MARION COUNTY, FLORIDA

PLAT BOOK 10, PAGE 203
SHEET 9 OF 9

CURVE TABLE						
NO.	DELTA	RADIUS	LENGTH	TANGENT	CHORD	C.B.
C31	742°39"	500.00'	67.29'	33.70'	67.24'	S04°11'59"W
C32	18°30'36"	500.00'	161.53'	81.47'	160.83'	S17°18'36"W
C33	49°40'47"	25.00'	21.68'	11.57'	21.00'	S51°24'18"W
C34	75°54'02"	60.00'	79.48'	46.79'	73.80'	N38°17'41"E
C35	89°59'59"	60.00'	94.25'	60.00'	84.85'	N44°39'20"W
C36	113°27'33"	60.00'	118.81'	91.44'	100.33'	S33°36'54"W
C37	49°40'47"	25.00'	21.68'	11.57'	21.00'	N01°43'31"E
C38	26°13'14"	560.00'	256.28'	130.42'	254.05'	N13°27'17"E

STATE PLANE COORDINATES:

POINT	NORTHING	EASTING	SCALE FACTOR
Q424	1689706.2443	660315.3325	0.999941196
COED 0028	1734962.9634	639104.6136	0.999941510
(F)	1716828.3502	661905.8583	0.999941216
(G)	1716823.9443	662909.9979	0.999941229
(H)	1715713.9567	662905.1314	0.999941229

NOTE:
10' UTILITY EASEMENT RESERVED ALONG
AND ADJACENT TO RIGHTS-OF-WAYS

LINE TABLE		
LINE	LENGTH	BEARING
L50	132.89'	N17°31'47"E
L51	191.50'	S21°10'40"W
L52	164.56'	S28°20'40"W
L53	118.09'	S38°15'06"W
L54	77.93'	S52°55'10"W
L55	79.99'	S67°00'42"W
L56	72.01'	S82°18'03"W
L57	51.00'	N82°50'26"W
L58	82.19'	S24°12'29"E
L59	109.30'	S07°13'11"E
L60	107.03'	S10°19'48"W
L61	103.84'	S28°13'07"W

100 YR. FLOOD ELEVATION = 64.0' +/-
ORDINARY HIGH WATER ELEVATION = 52.76'

GRAPHIC SCALE

(IN FEET)
1 inch = 60 ft.

R.M. BARRINEAU & ASSOCIATES, INC.

PROFESSIONAL SURVEYORS & MAPPERS
OAKHURST PROFESSIONAL PARK
1309 S.E. 25TH LOOP, SUITE 103 PHONE (352) 622-3133
OCALA, FLORIDA 34471 FAX (352) 369-3771
RESIDUAL M. BARRINEAU, P.S.M. - FOUNDER
CERTIFICATE OF AUTHORIZATION NO. LB 5091
KEVIN J. FLANAGAN, P.S.M. - LS 3842 CHRISTOPHER J. HOWSON, P.S.M. - LS 6953
WELVIN A. BOWEN, P.S.M. - LS 5035

LEGEND: UNLESS OTHERWISE NOTED

- = PERMANENT REFERENCE MONUMENT
SET 4"x4" CONCRETE MONUMENT NO LB5091
- = PERMANENT REFERENCE MONUMENT
FOUND 4"x4" CONCRETE MONUMENT
I.D. - MOOREHEAD ENGINEERING COMPANY
- = PERMANENT CONTROL POINT
SET NAIL & DISK I.D. - LB5091
- R/W = RIGHT-OF-WAY
- (NR) = NON-RADIAL
- = CENTERLINE OF RIGHT OF WAY
- - - = BREAKLINE NOT TO SCALE
- O.R. = OFFICIAL RECORDS
- P.R.C. = POINT OF REVERSE CURVATURE
- P.C. = POINT OF CURVATURE
- P.T. = POINT OF TANGENCY
- I.D. = IDENTIFICATION
- (R) = RADIAL LINE
- (TYP) = TYPICAL
- D.E. = DRAINAGE EASEMENT
- U.E. = UTILITY EASEMENT
- D.R.A. = DRAINAGE RETENTION AREA
- = DRIVEWAY PROHIBITED WITHIN THIS AREA
- = LANDSCAPE BUFFER
- = DENOTES BUILDABLE AREA
- - - = DENOTES MEANDER LINE

THE WEST BOUNDARY OF
GOVERNMENT LOT 3, SECTION
35, TOWNSHIP 16 SOUTH,
RANGE 23 EAST

MATCHLINE - SEE SHEET 7

MATCHLINE - SEE SHEET 6

THE EAST BOUNDARY OF GOVERNMENT LOT 3, SECTION 35,
TOWNSHIP 16 SOUTH, RANGE 23 EAST
NOT PLATTED

(3179.30' TOTAL)

NOT PLATTED