


AVONLEA PHASE 1 REPLAT OF LOT 19


(A HAMLET SUBDIVISION)
A REPLAT OF LOT 19, AVONLEA PHASE 1, AS RECORDED IN PLAT BOOK 10, PAGES 195 THROUGH 203, OF THE PUBLIC RECORDS
OF MARION COUNTY, FLORIDA
SECTION 35, TOWNSHIP 16 SOUTH, RANGE 23 EAST
MARION COUNTY, FLORIDA

PLAT BOOK 15, PAGE 11
SHEET 2 OF 2

POINT	NORTHING	EASTING	SCALE FACTOR
(A)	1716016.5939	662310.6719	0.99994121
(B)	1716170.2165	662358.2736	0.99994122
(C)	1716244.8282	662395.4262	0.99994122
(D)	1716257.9586	662411.8240	0.99994122
(E)	1716319.9585	662457.4601	0.99994122
(F)	1716313.9926	662907.4555	0.99994122
(G)	1716013.9954	662906.1452	0.99994122

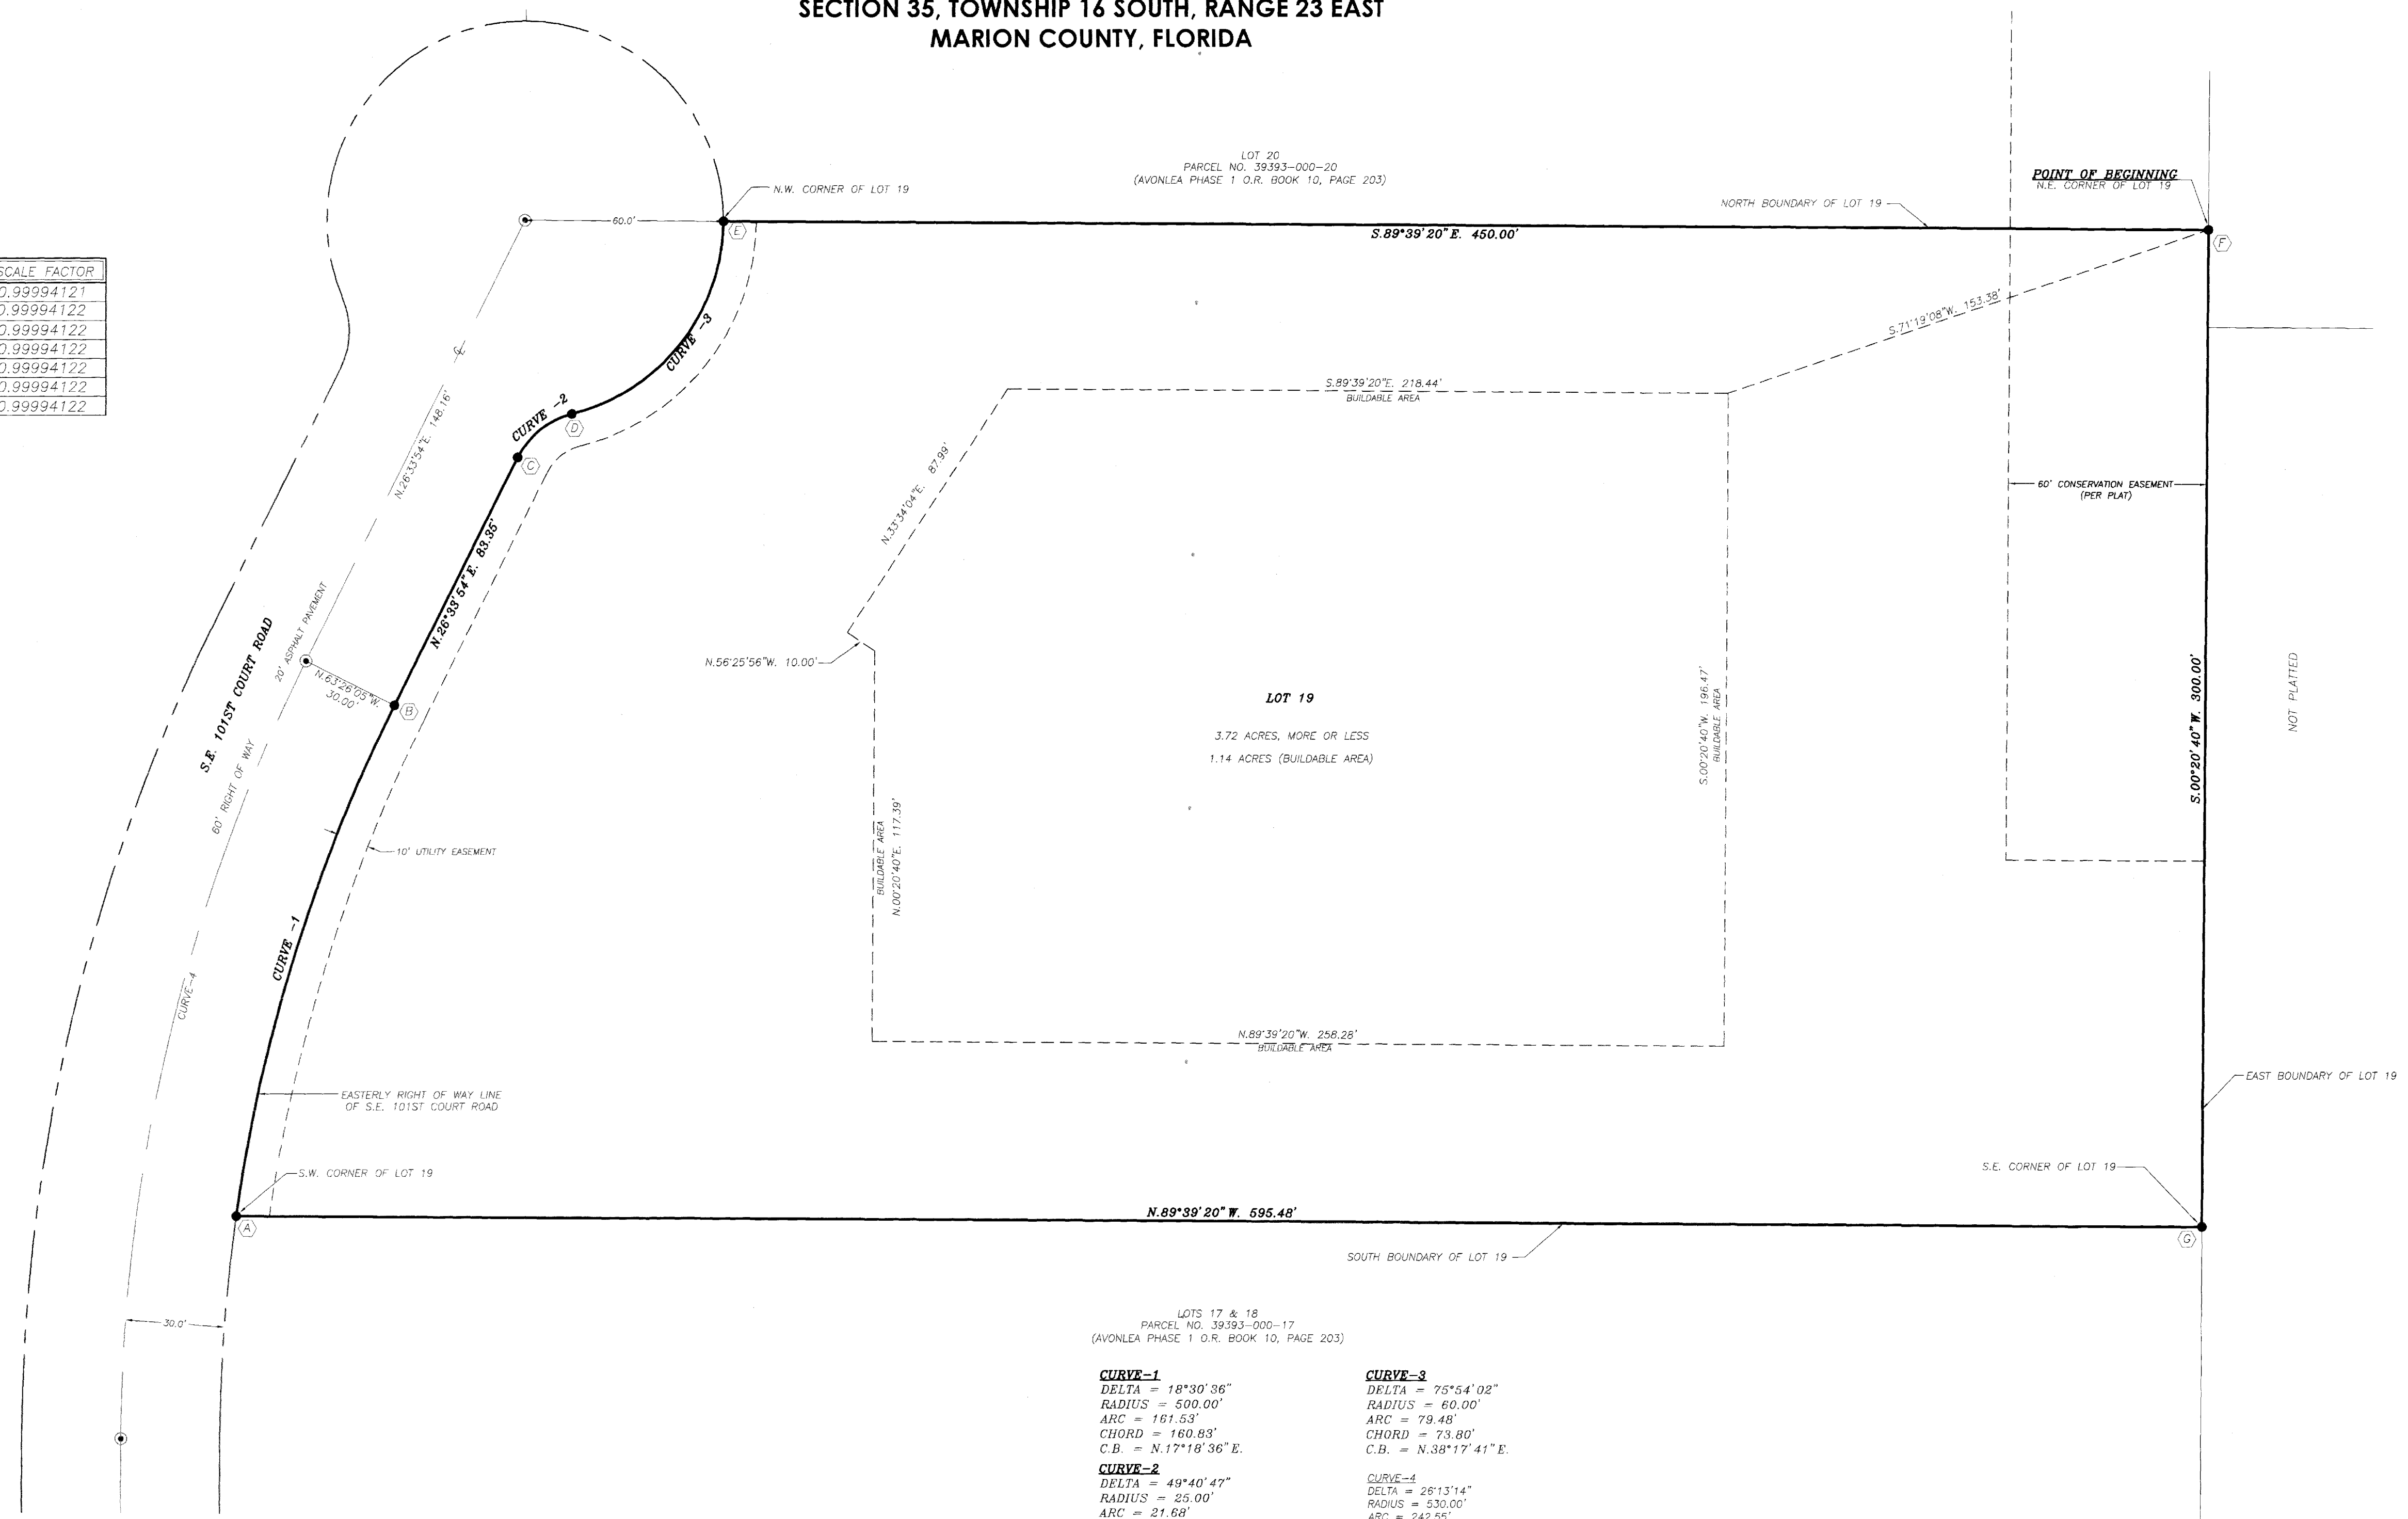

- LEGEND** UNLESS OTHERWISE NOTED
- CL = CENTERLINE OF RIGHT OF WAY
 - C.B. = CHORD BEARING
 - O.R. = OFFICIAL RECORDS OF MARION COUNTY
 - (A) = STATE PLANE COORDINATE
 - = FOUND 5/8" IRON ROD & CAP - LB 5091
 - ⊙ = FOUND NAIL & DISK - PCP LB 5091
 - (F) = FIELD MEASUREMENT
 - (C) = CALCULATED DIMENSION
 - ⊙ = SANITARY CLEANOUT
 - ⊙ = SANITARY MANHOLE
 - ⊙ = DRAINAGE MANHOLE
 - ⊙ = STORM DRAINAGE GRATE
 - ⊙ = WATER METER
 - ⊙ = WATER VALVE
 - ⊙ = FIRE HYDRANT
 - ⊙ = MAILBOX
 - ⊙ = SIGN
 - P.V.C. = POLYVINYL CHLORIDE
 - R.C.P. = REINFORCED CONCRETE PIPE
 - C.M.P. = CORRUGATED METAL PIPE
 - A/E = AERIAL ELECTRIC
 - = BROKEN LINE; NOT DRAWN TO SCALE
 - ⊙ = DENOTES CONCRETE
 - ⊙ = DENOTES ASPHALT

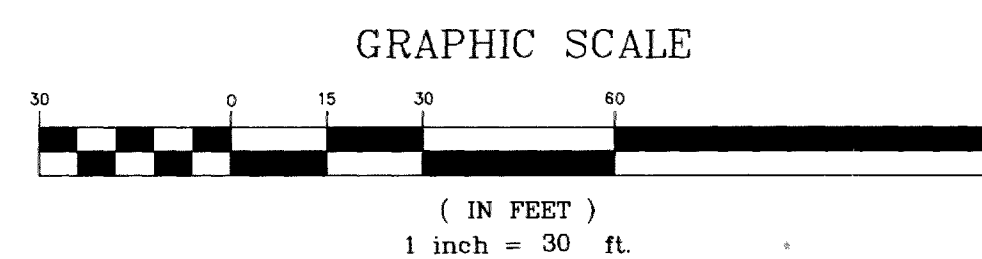

SURVEYOR'S CERTIFICATE:

I CERTIFY THIS PLAT, PREPARED UNDER MY DIRECTION AND SUPERVISION, COMPLIES WITH THE REQUIREMENTS OF CHAPTER 177, FLORIDA STATUTES, MEETS THE STANDARDS OF PRACTICE SET FORTH BY THE FLORIDA BOARD OF PROFESSIONAL SURVEYORS AND MAPPERS, AND IS IN ACCORDANCE WITH THE REQUIREMENTS OF THE MARION COUNTY LAND DEVELOPMENT CODE, AND THAT THIS PLAT DOES NOT ADVERSELY AFFECT THE LEGAL ACCESS OF ADJACENT PARCELS.

BY: *Travis P. Barrineau*
TRAVIS P. BARRINEAU, P.S.M.
FLORIDA REGISTERED SURVEYOR NO. LS 6897
R.M. BARRINEAU & ASSOCIATES, INC.

CERTIFICATE OF AUTHORIZATION NO. LB 5091
1309 S.E. 25TH LOOP, SUITE 103, OCALA, FLORIDA 34471

